



SRDR ROBOTİK

TEL : +90 552 442 77 37

MAİL: info@srdrobotik.com

ADRES : Ataşehir Ferhat Paşa, 35. Sk. No:42, 34844
Ataşehir / İSTANBUL



Firma İsmi : Birinci Otomotiv San. ve Tic.
Firma Kodu :
Firma Adresi : TAYSAD Organize Sanayi, 2. Cadde, NO:1 41420
Şekerpınar Çayırova Kocaeli / Türkiye
TEL : +90 262 723 42 00
FAX :

Pano Ebat : 80X120
Pano Koruma Sınıfı : IP 65
Toplam güç : 20 A
Besleme : 400 V
Kumanda Gerilimi : 24 V



Sipariş Tarihi : 16.05.2022
Proje teslim Tarihi :


Pano Montaj Sorumlusu : SENAN ERMEYDAN
Proje Sorumlusu : SERDAR GÜVENSOY

Proje Numarasi :

Toplam Sayfa Sayısı :27

SİPARİŞ TARİHİ		 SRDR ROBOTİK TEL: +90 552 442 77 37 ADRES: Bağlarbaşı Mah. Yonca Sk. No:1 Kat:3/6 34844 Maltepe/İSTANBUL e-mail : info@srdrobotik.com	PROJE NO:		KONTROL EDEN İMZA:	EK AÇIKLAMA:	1 KAPAK	
GÜNCELLEME TARİHİ	2.01.2023		KONTOL EDEN:				TOPLAM SAYFA SAYISI:	27
PROJE SORUMLUSU							ÖNCEKİ SAYFA:	
MONTAJ SORUMLUSU							SÖNRAKİ SAYFA:	2 Pano Ön Görünümü

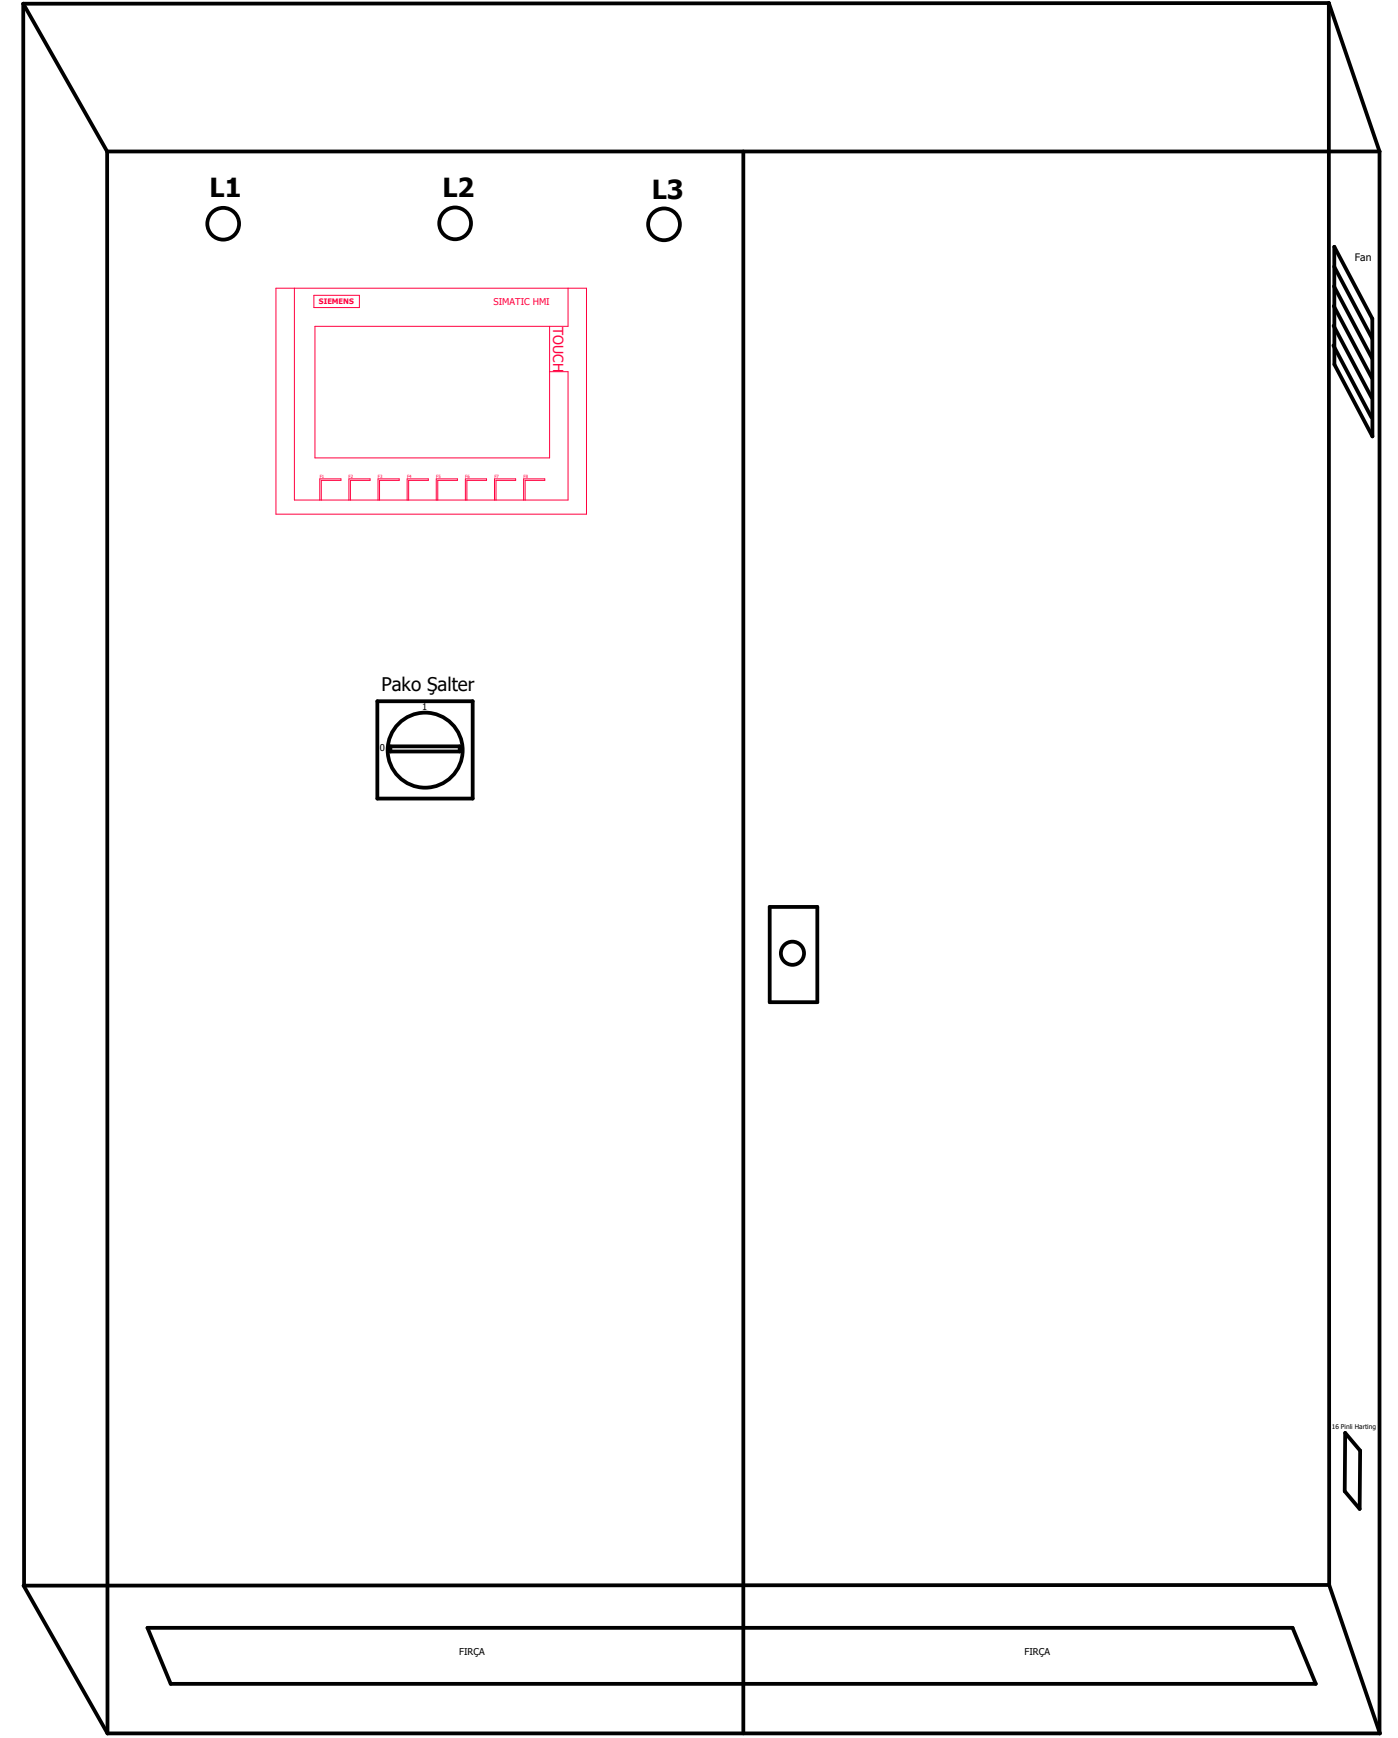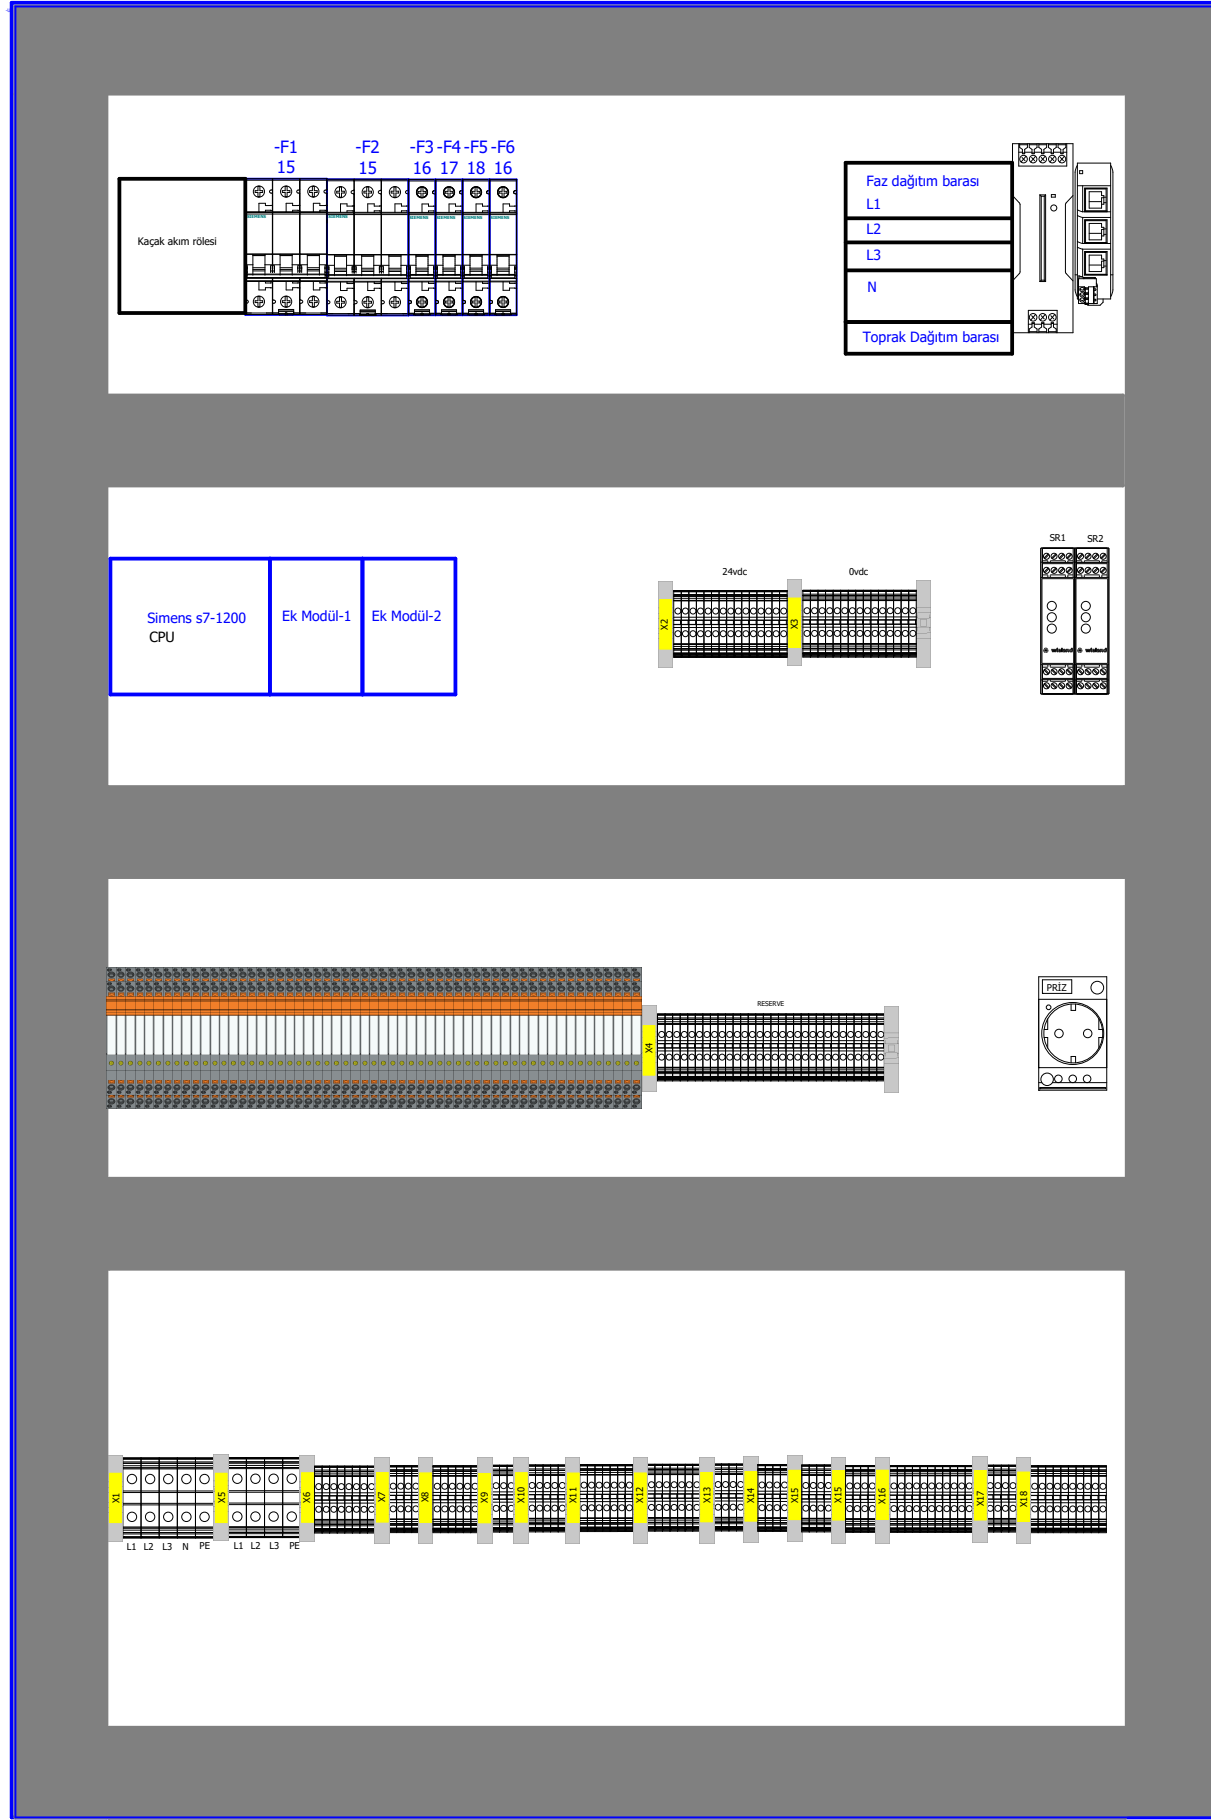

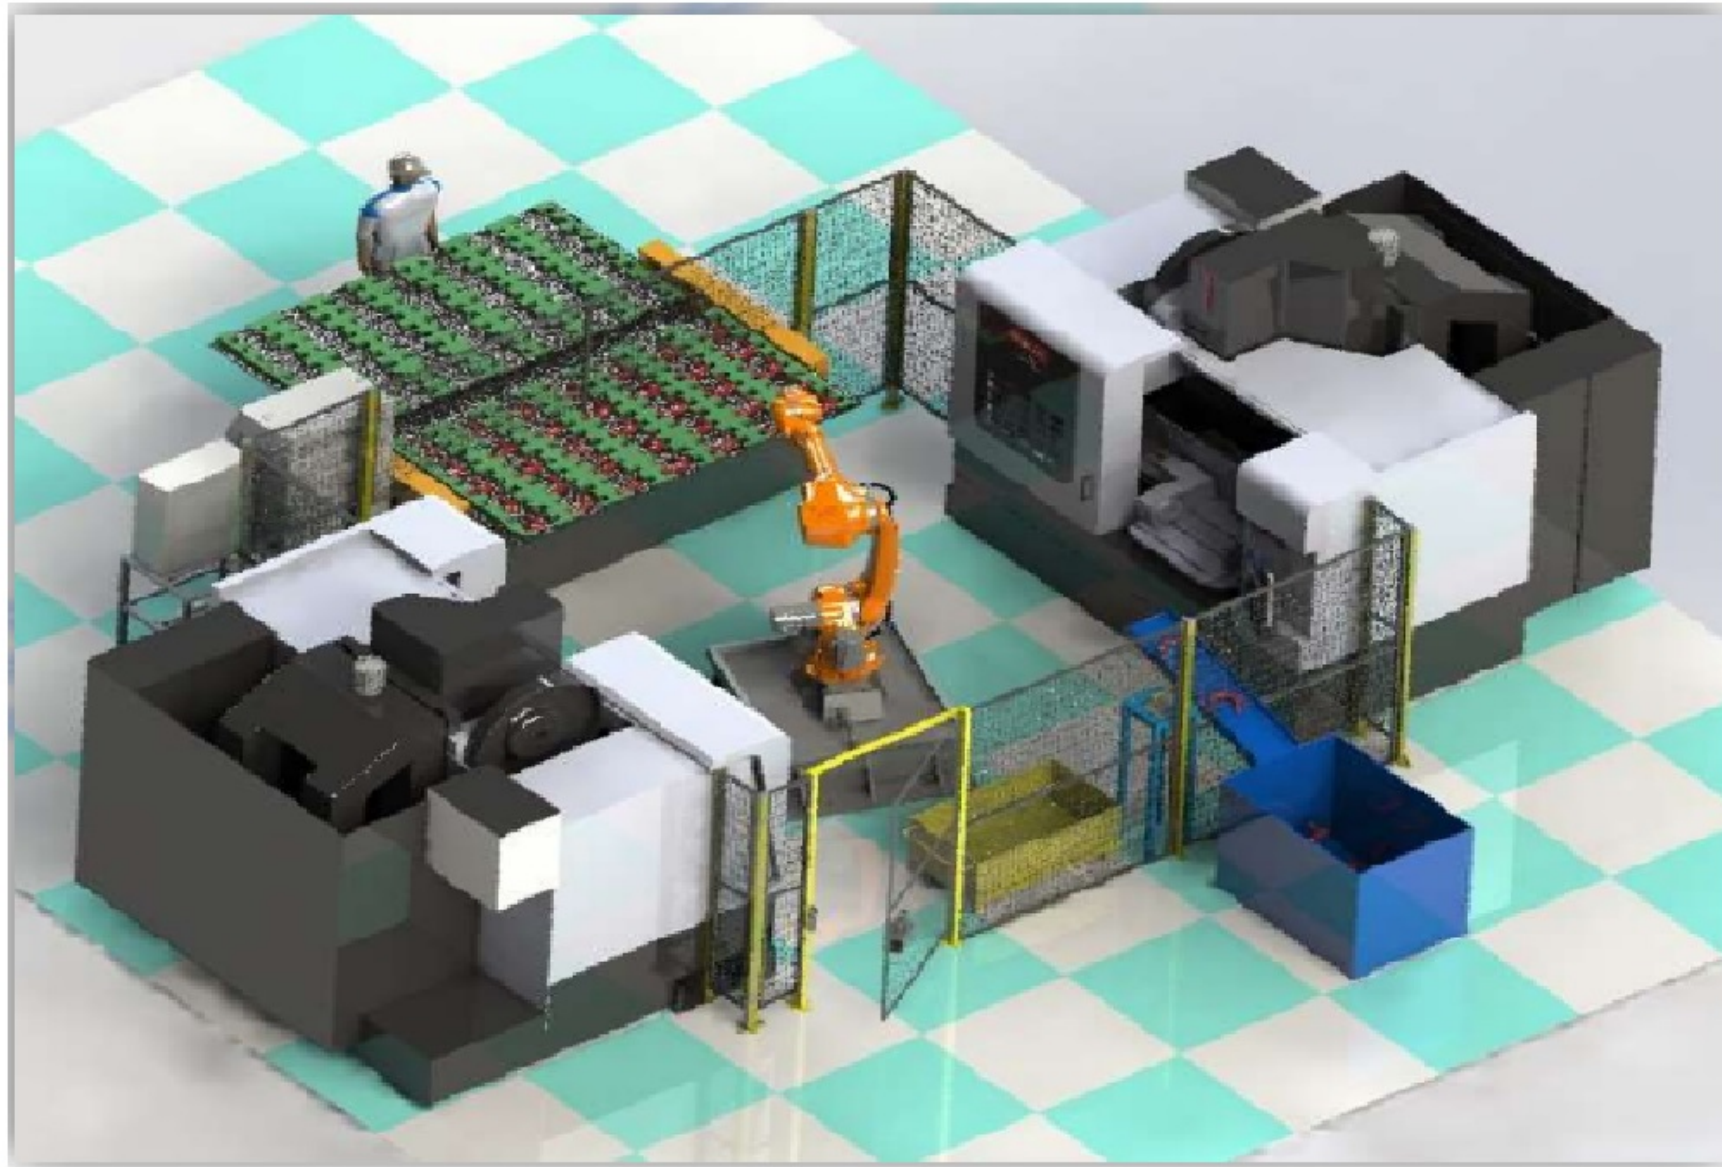

SİPARİŞ TARİHİ	
GÜNCELLEME TARİHİ	2.01.2023
PROJE SORUMLUSU	
MONTAJ SORUMLUSU	



SRDR ROBOTİK
TEL: +90 552 442 77 37
ADRES: Bağlarbaşı Mah. Yonca Sk. No:1 Kat:3/6 34844 Maltepe/İSTANBUL
e-mail : info@sdrrobotik.com

PROJE NO:



KONTROL EDEN:

KONTROL EDEN İMZA:


EK AÇIKLAMA:

3 LAYOUT


TOPLAM SAYFA SAYISI:	27
ÖNCEKİ SAYFA:	2 Pano Ön Görünümü
SONRAKİ SAYFA:	4 GÜÇ DEVRESİ

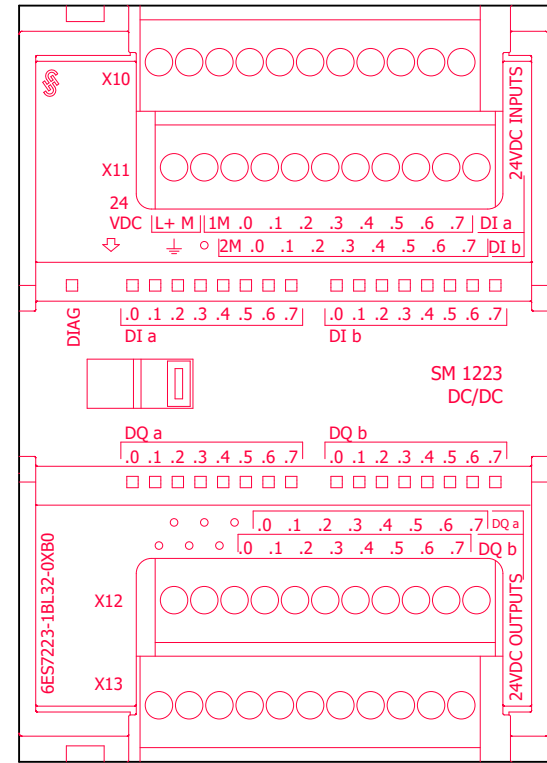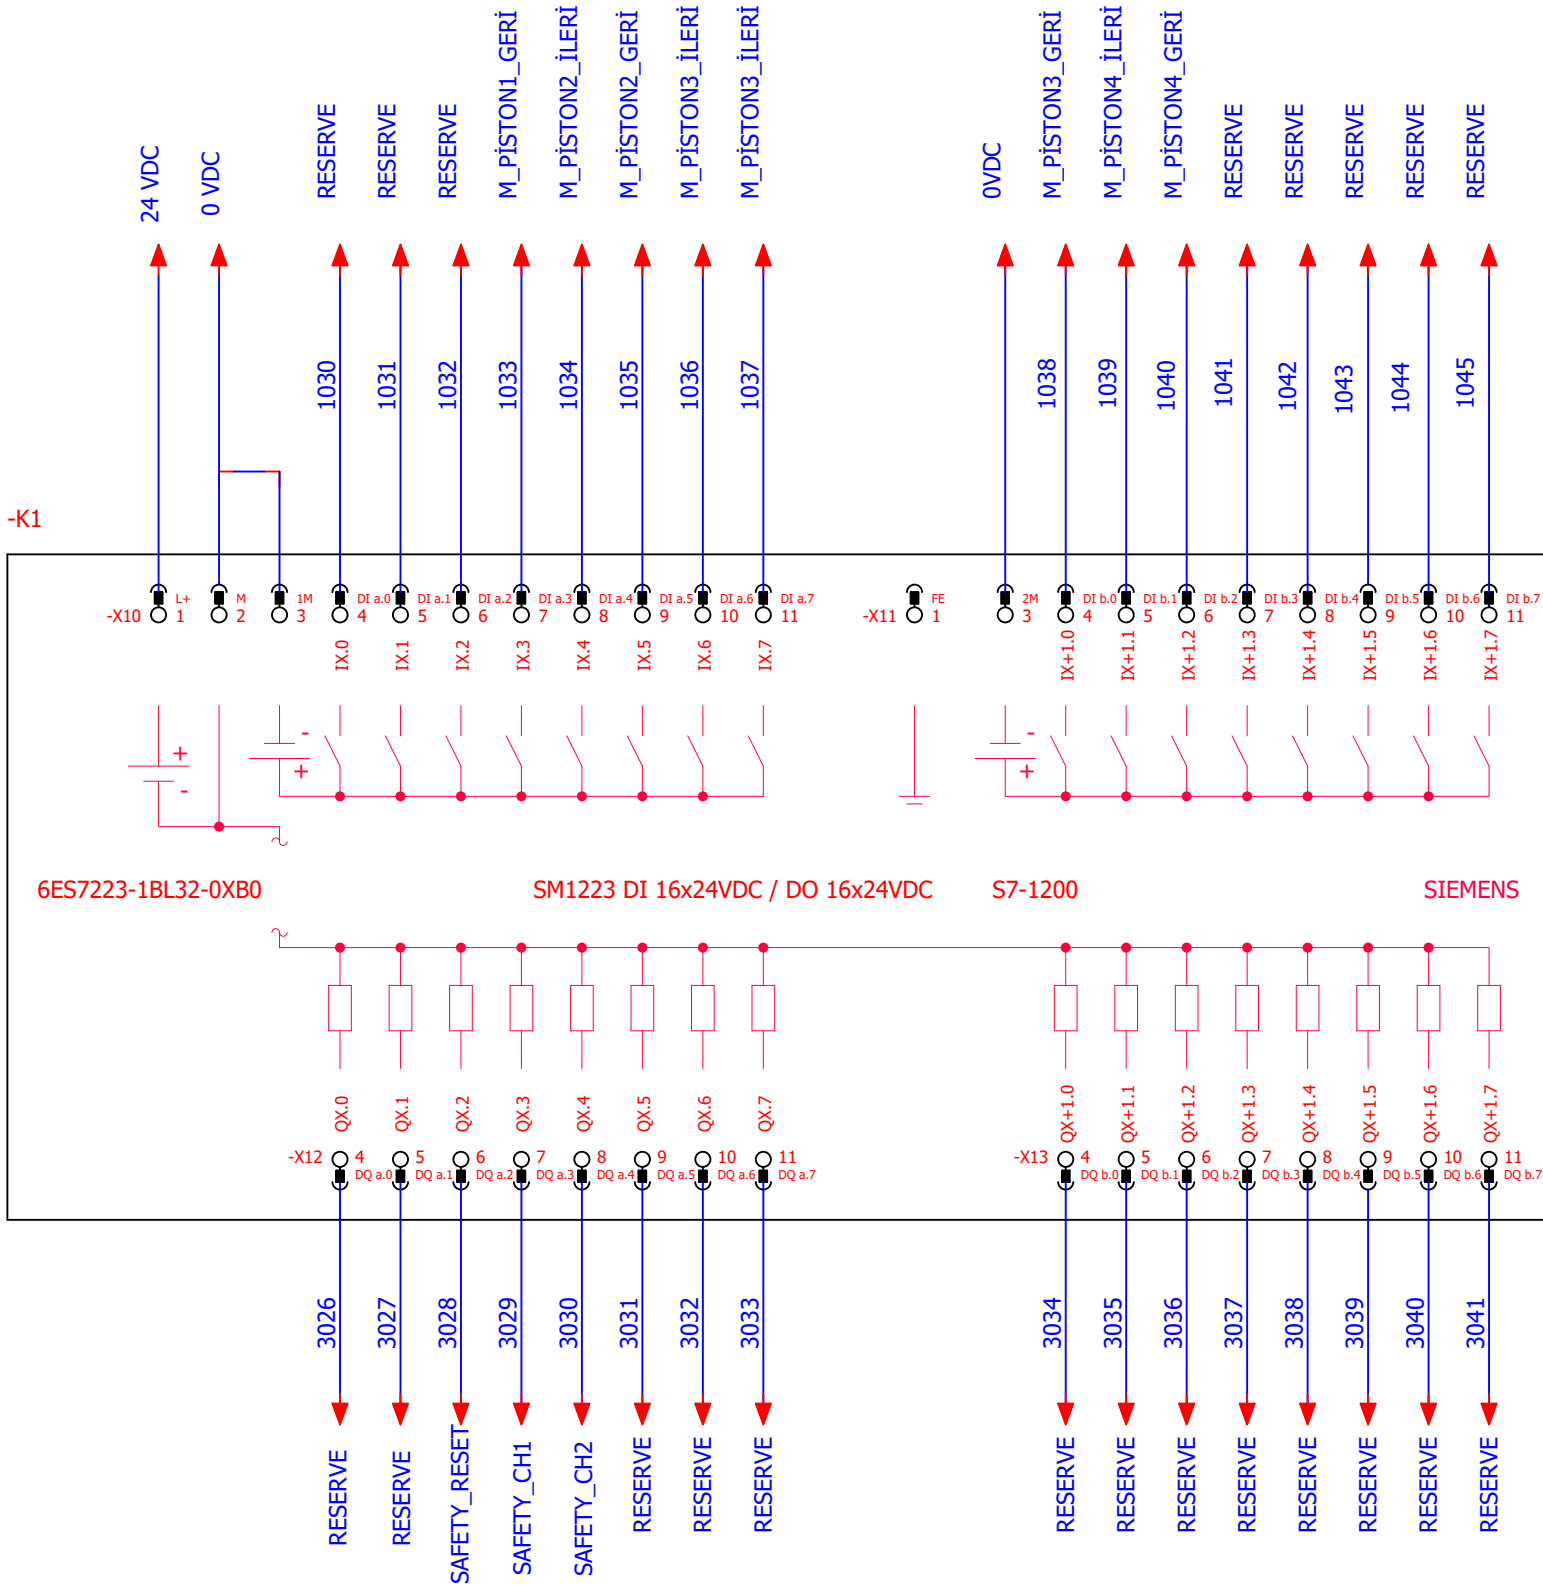

-K1

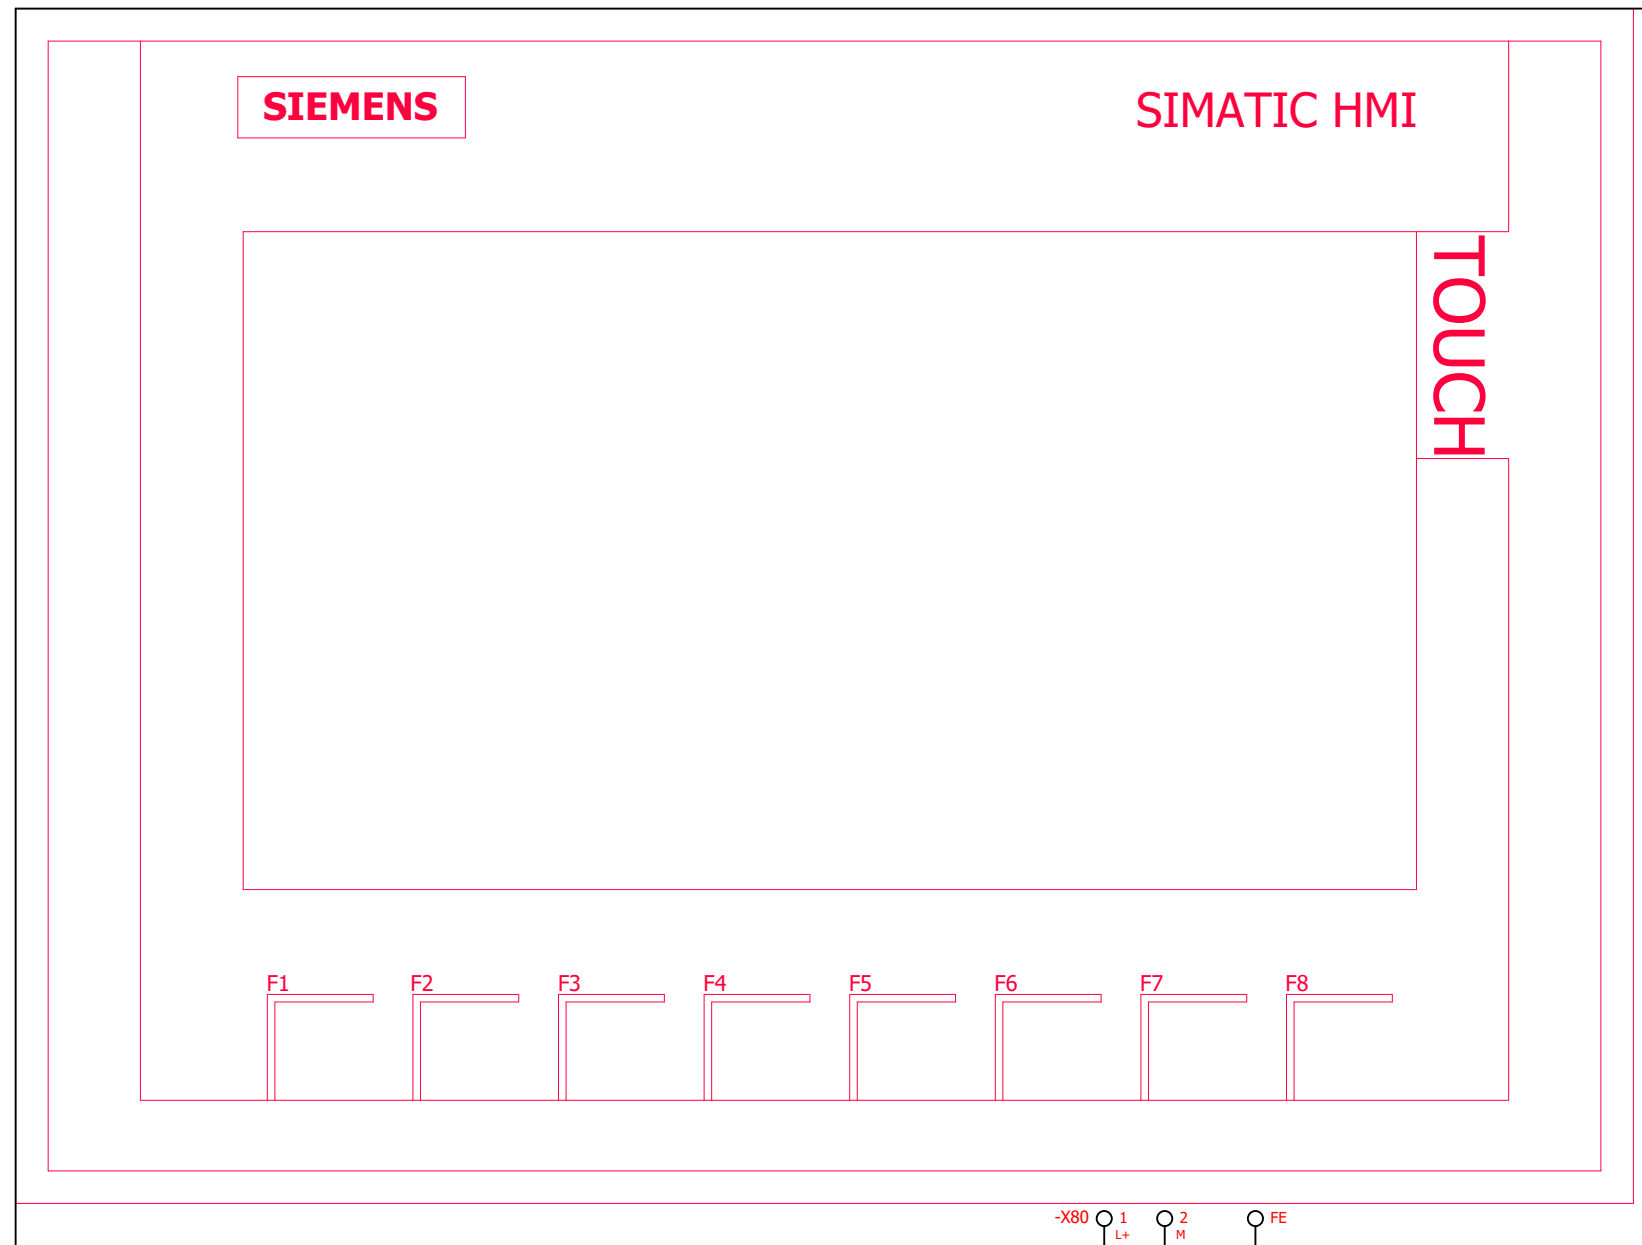

-K1

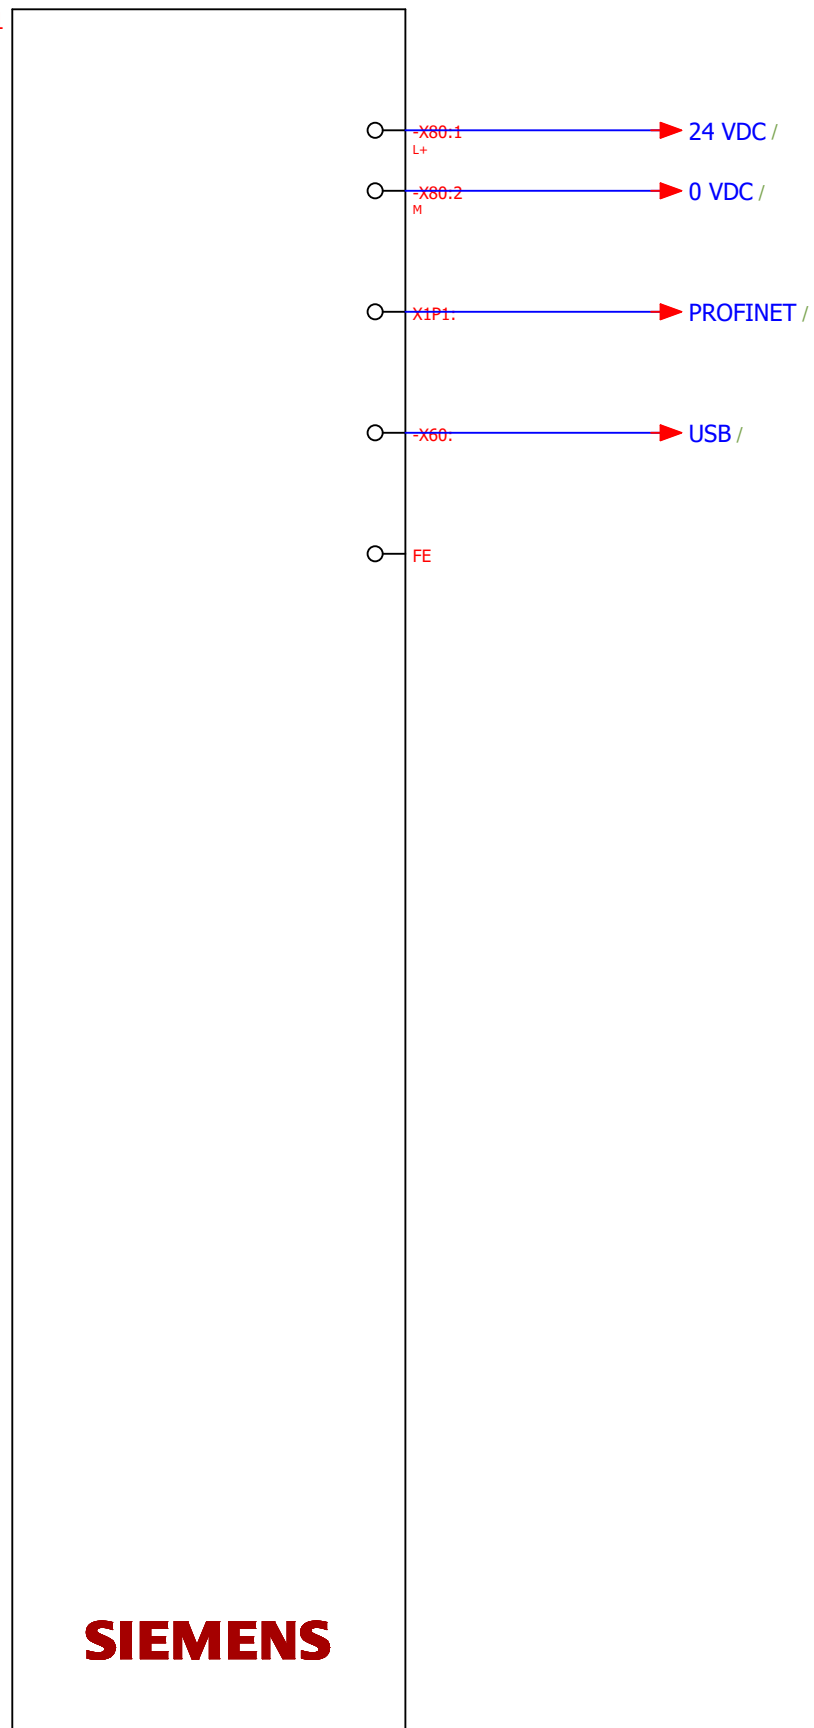


SİPARİŞ TARİHİ	
GÜNCELLEME TARİHİ	2.01.2023
PROJE SORUMLUSU	
MONTAJ SORUMLUSU	


	SRDR ROBOTİK TEL: +90 552 442 77 37 ADRES: Bağlarbaşı Mah. Yonca Sk. No:1 Kat:3/6 34844 Maltepe/İSTANBUL e-mail : info@srdrobotik.com
---	--


PROJE NO:	
KONTOL EDEN:	


KONTROL EDEN İMZA:	EK AÇIKLAMA:

TOPLAM SAYFA SAYISI:	27
ÖNCEKİ SAYFA:	6 EK MODÜL2
SÖNRAKİ SAYFA:	8 ETHERNET SWITCH

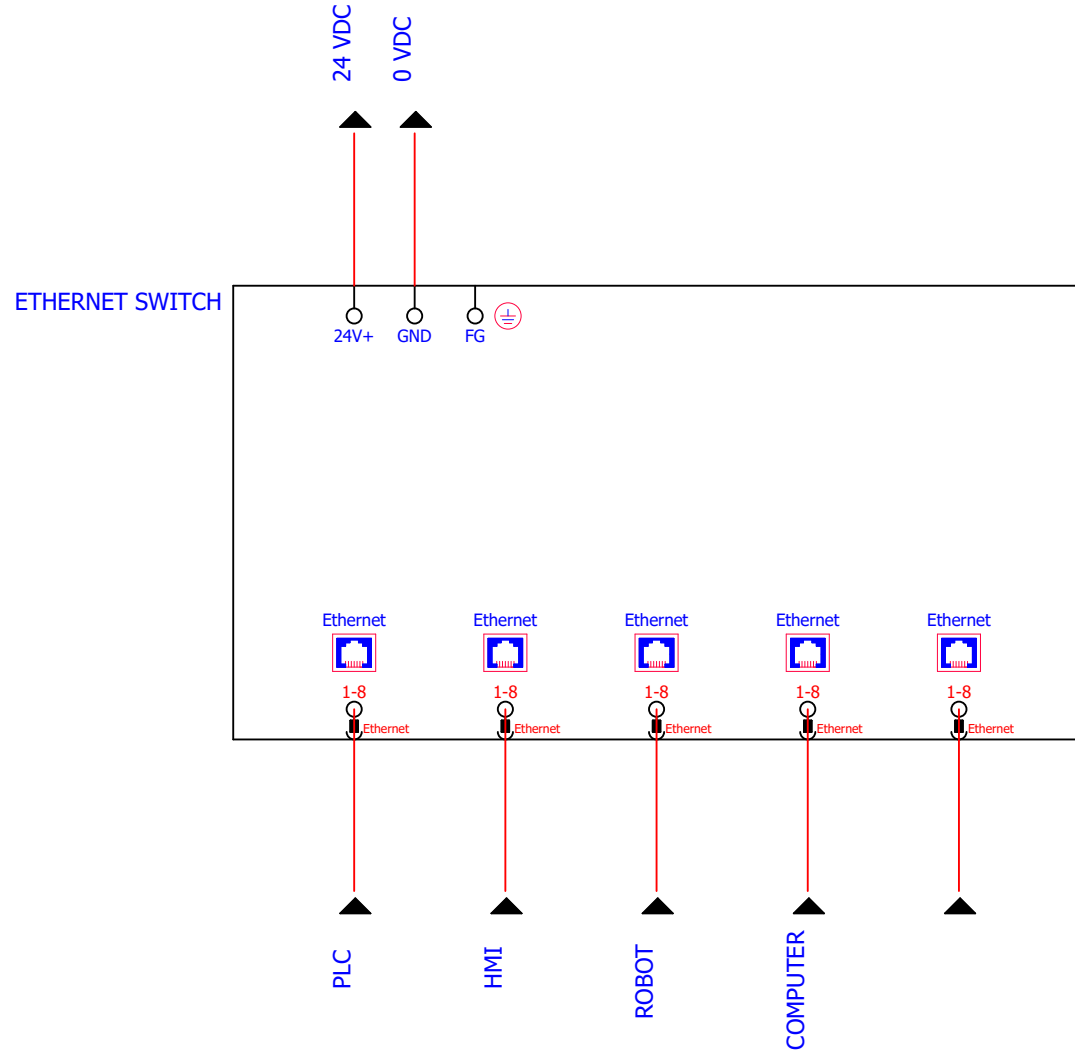


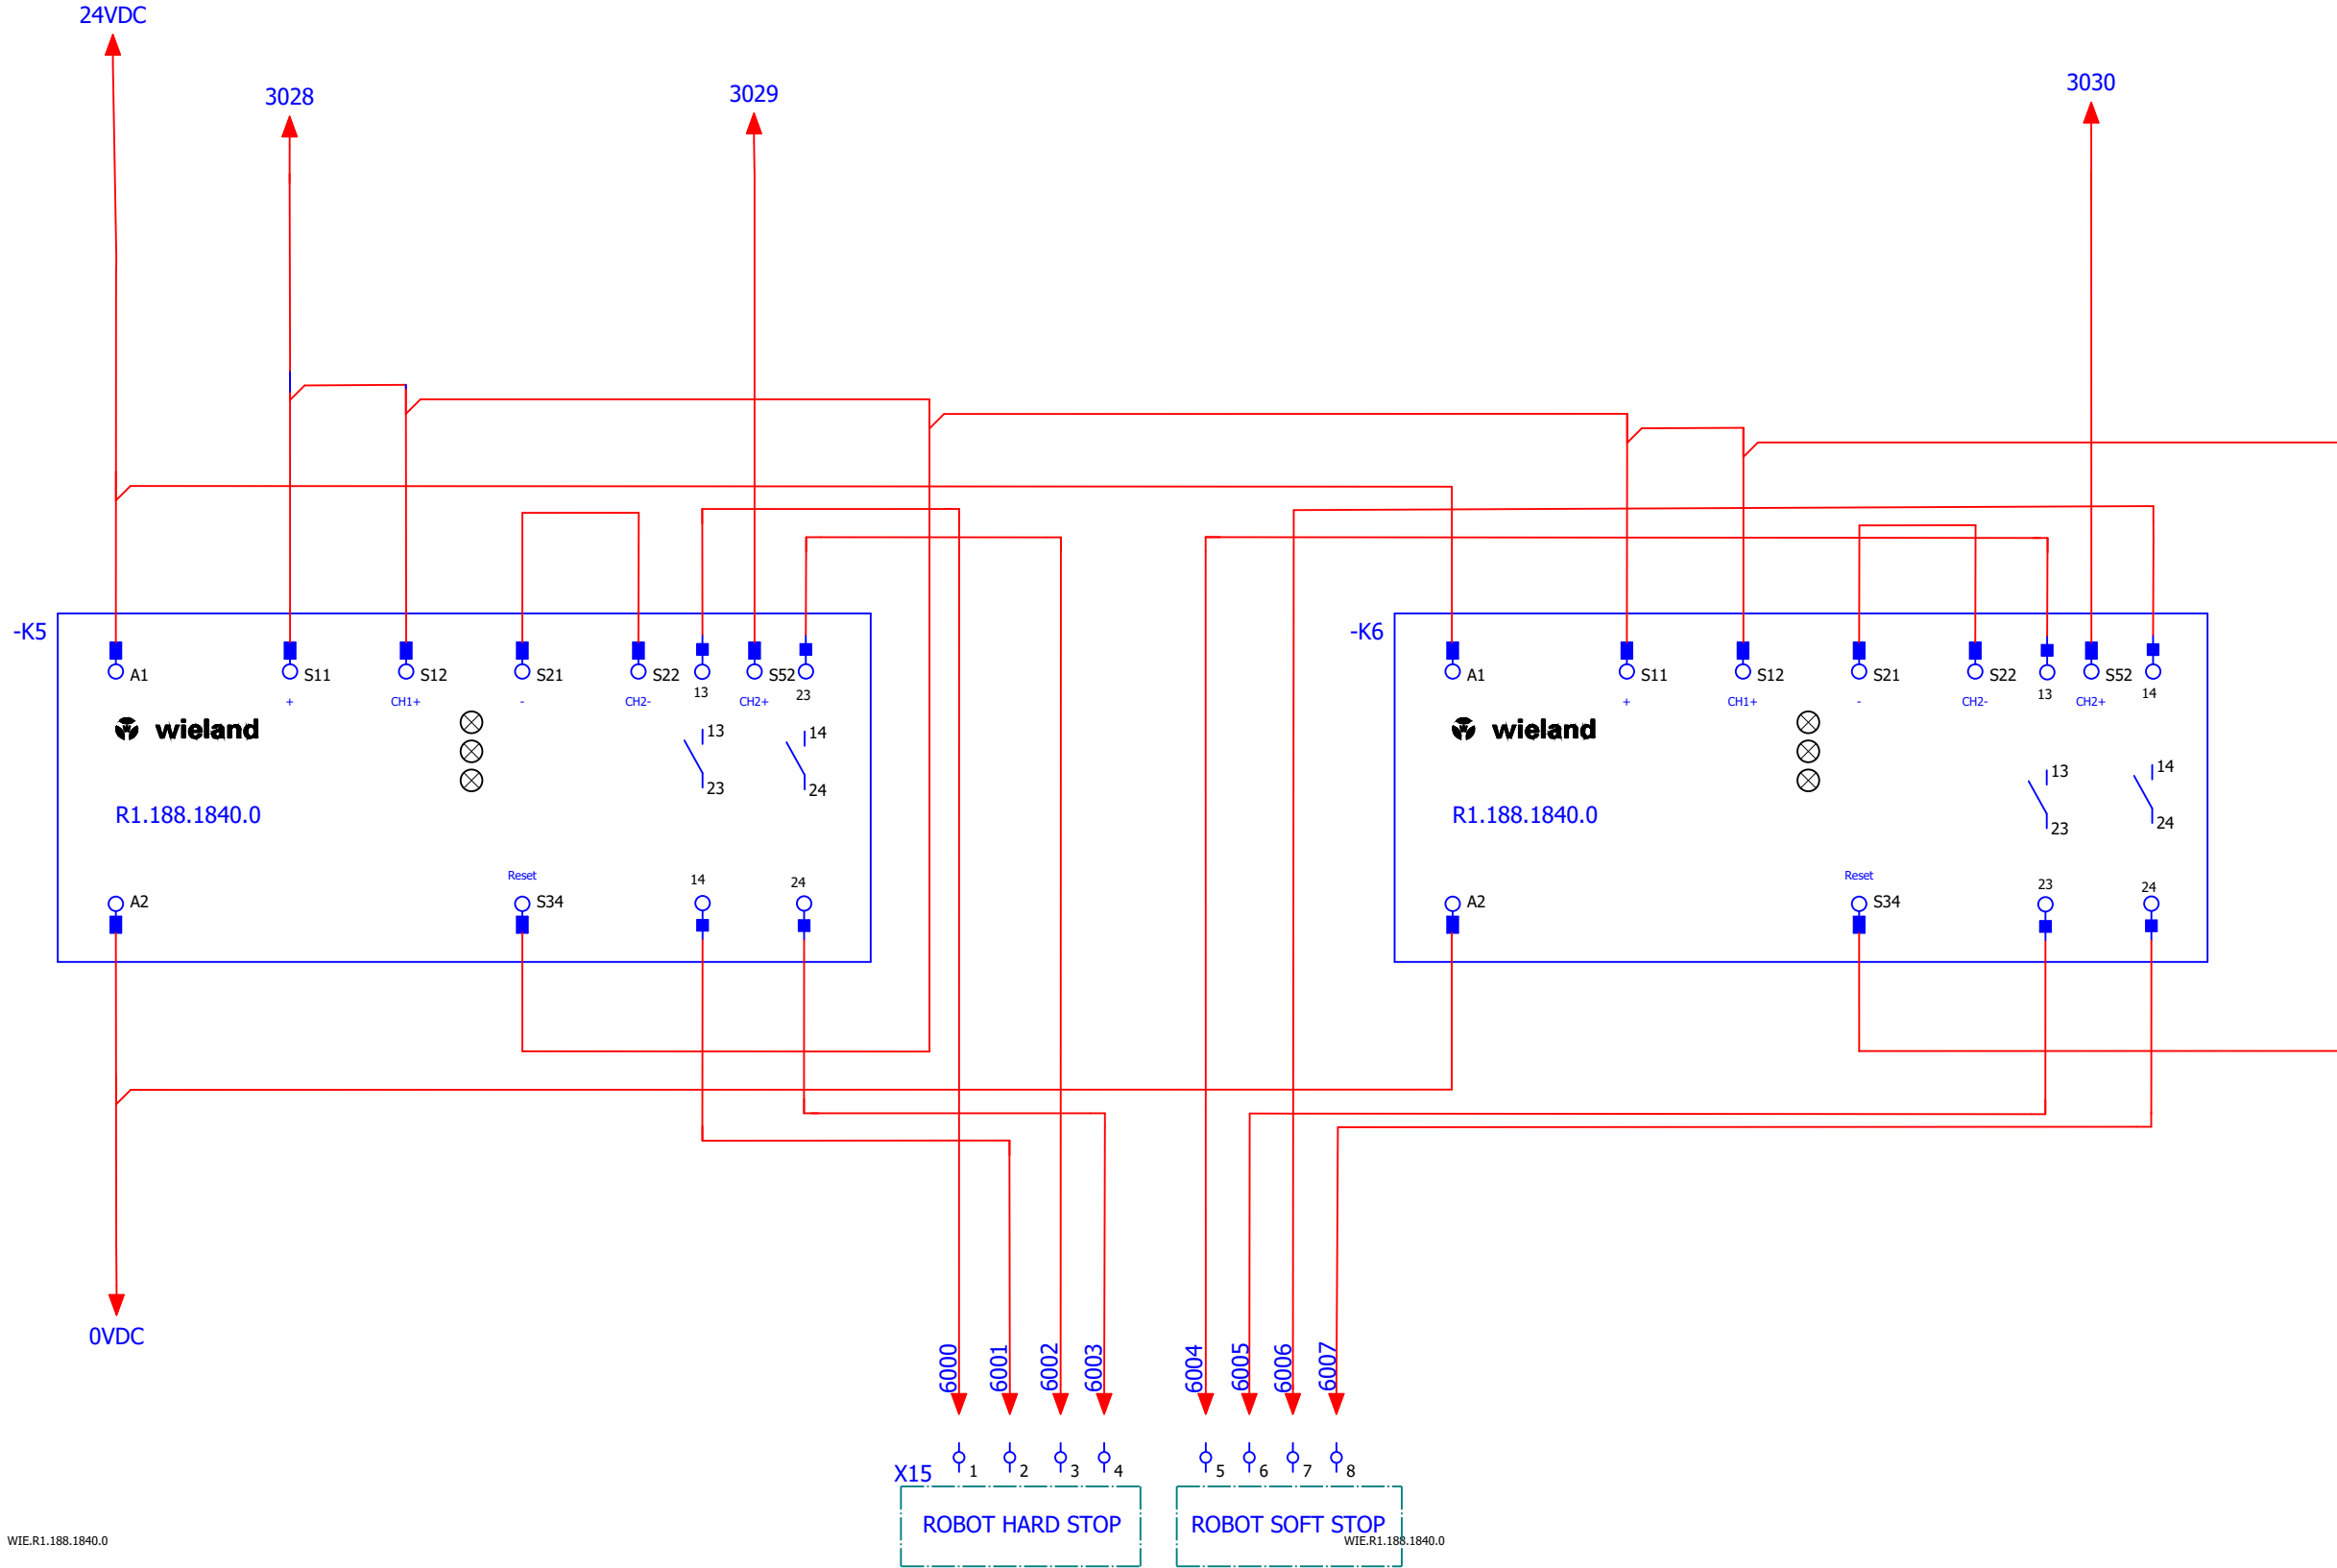

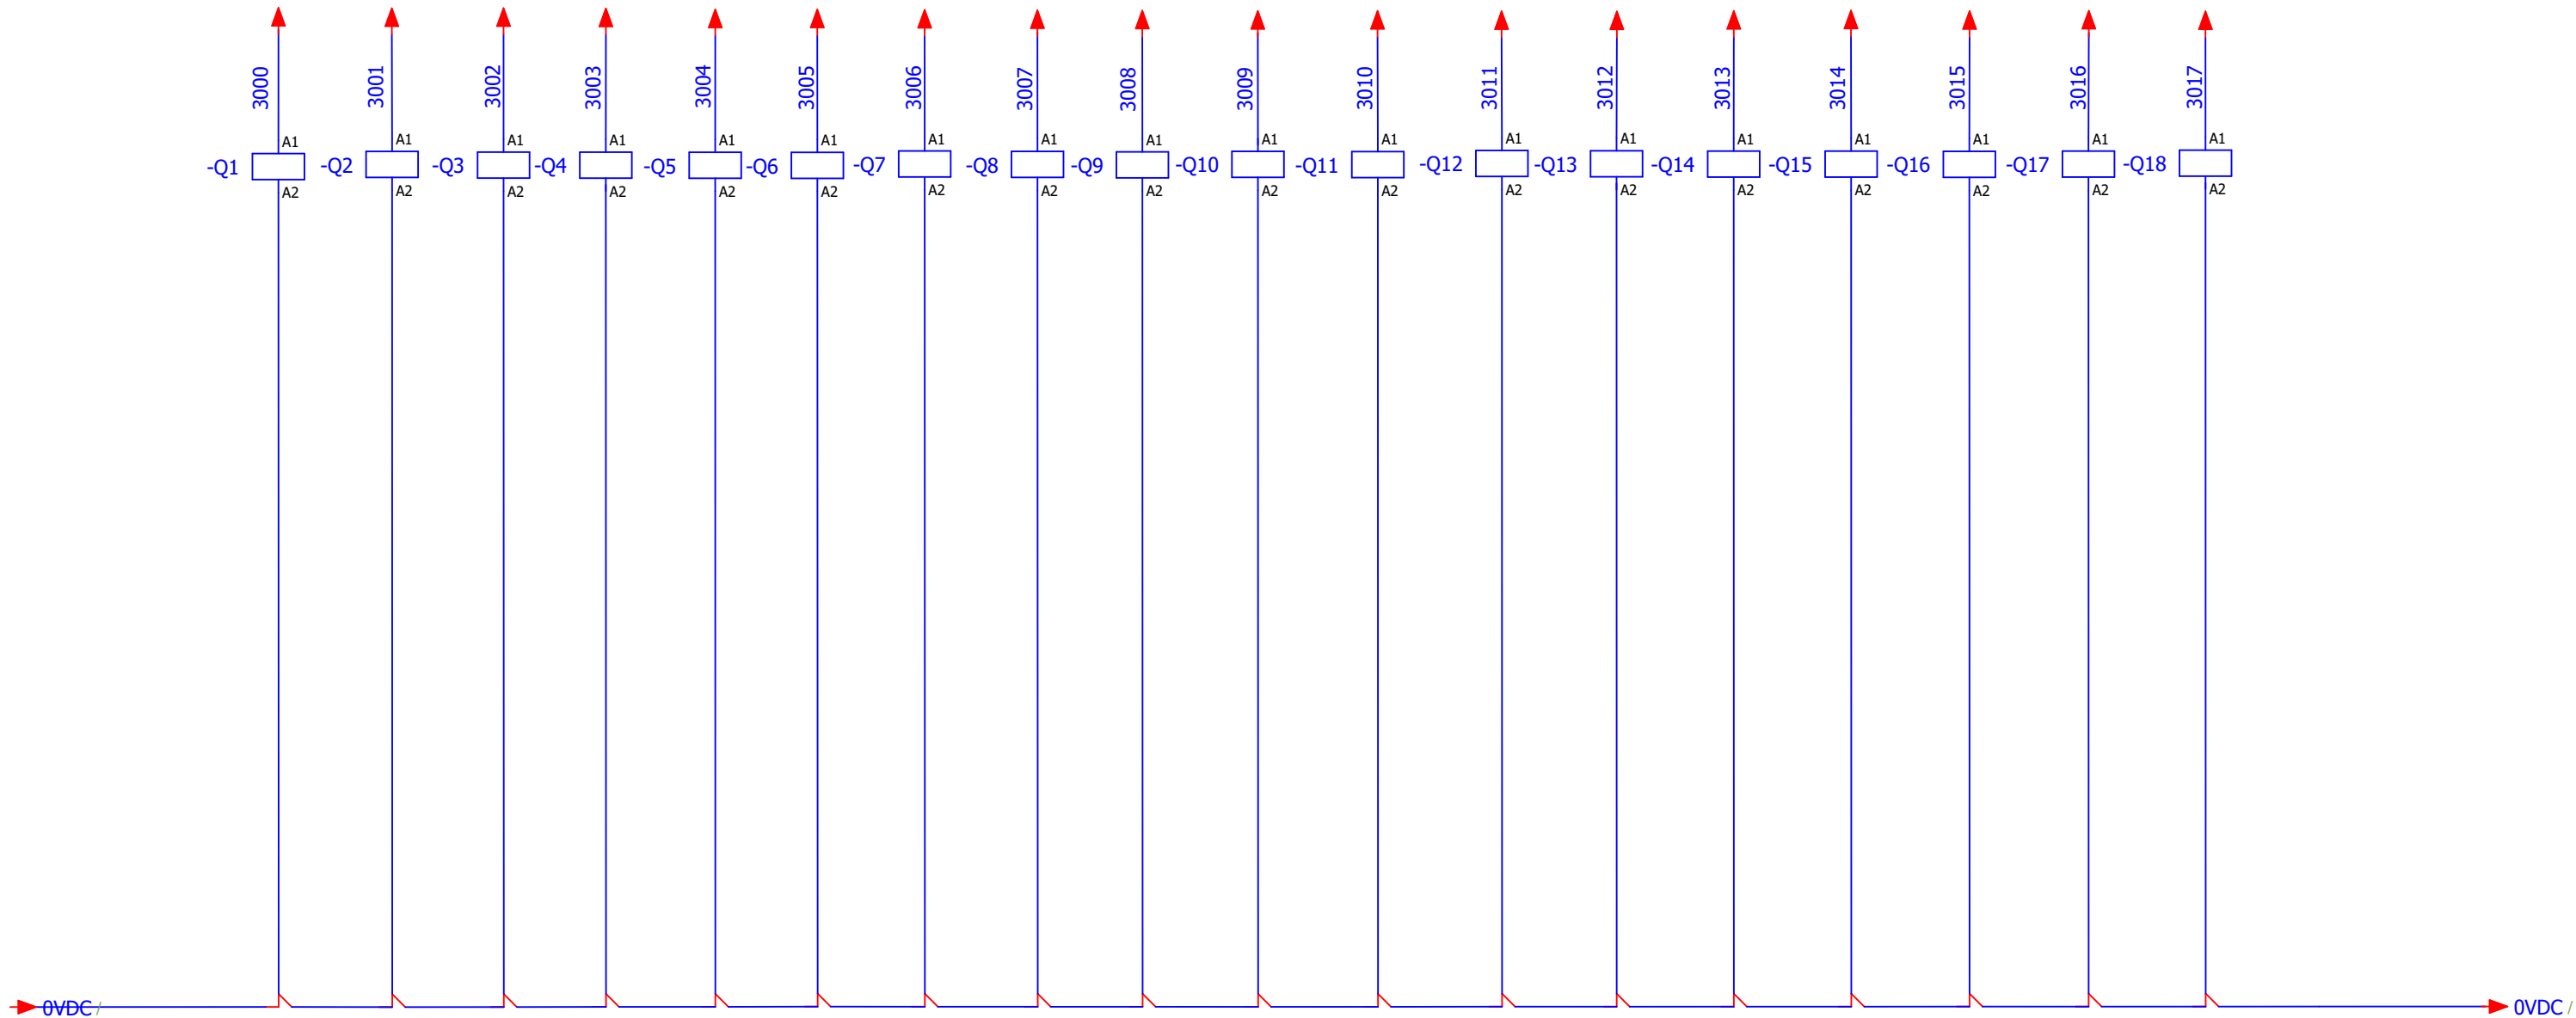


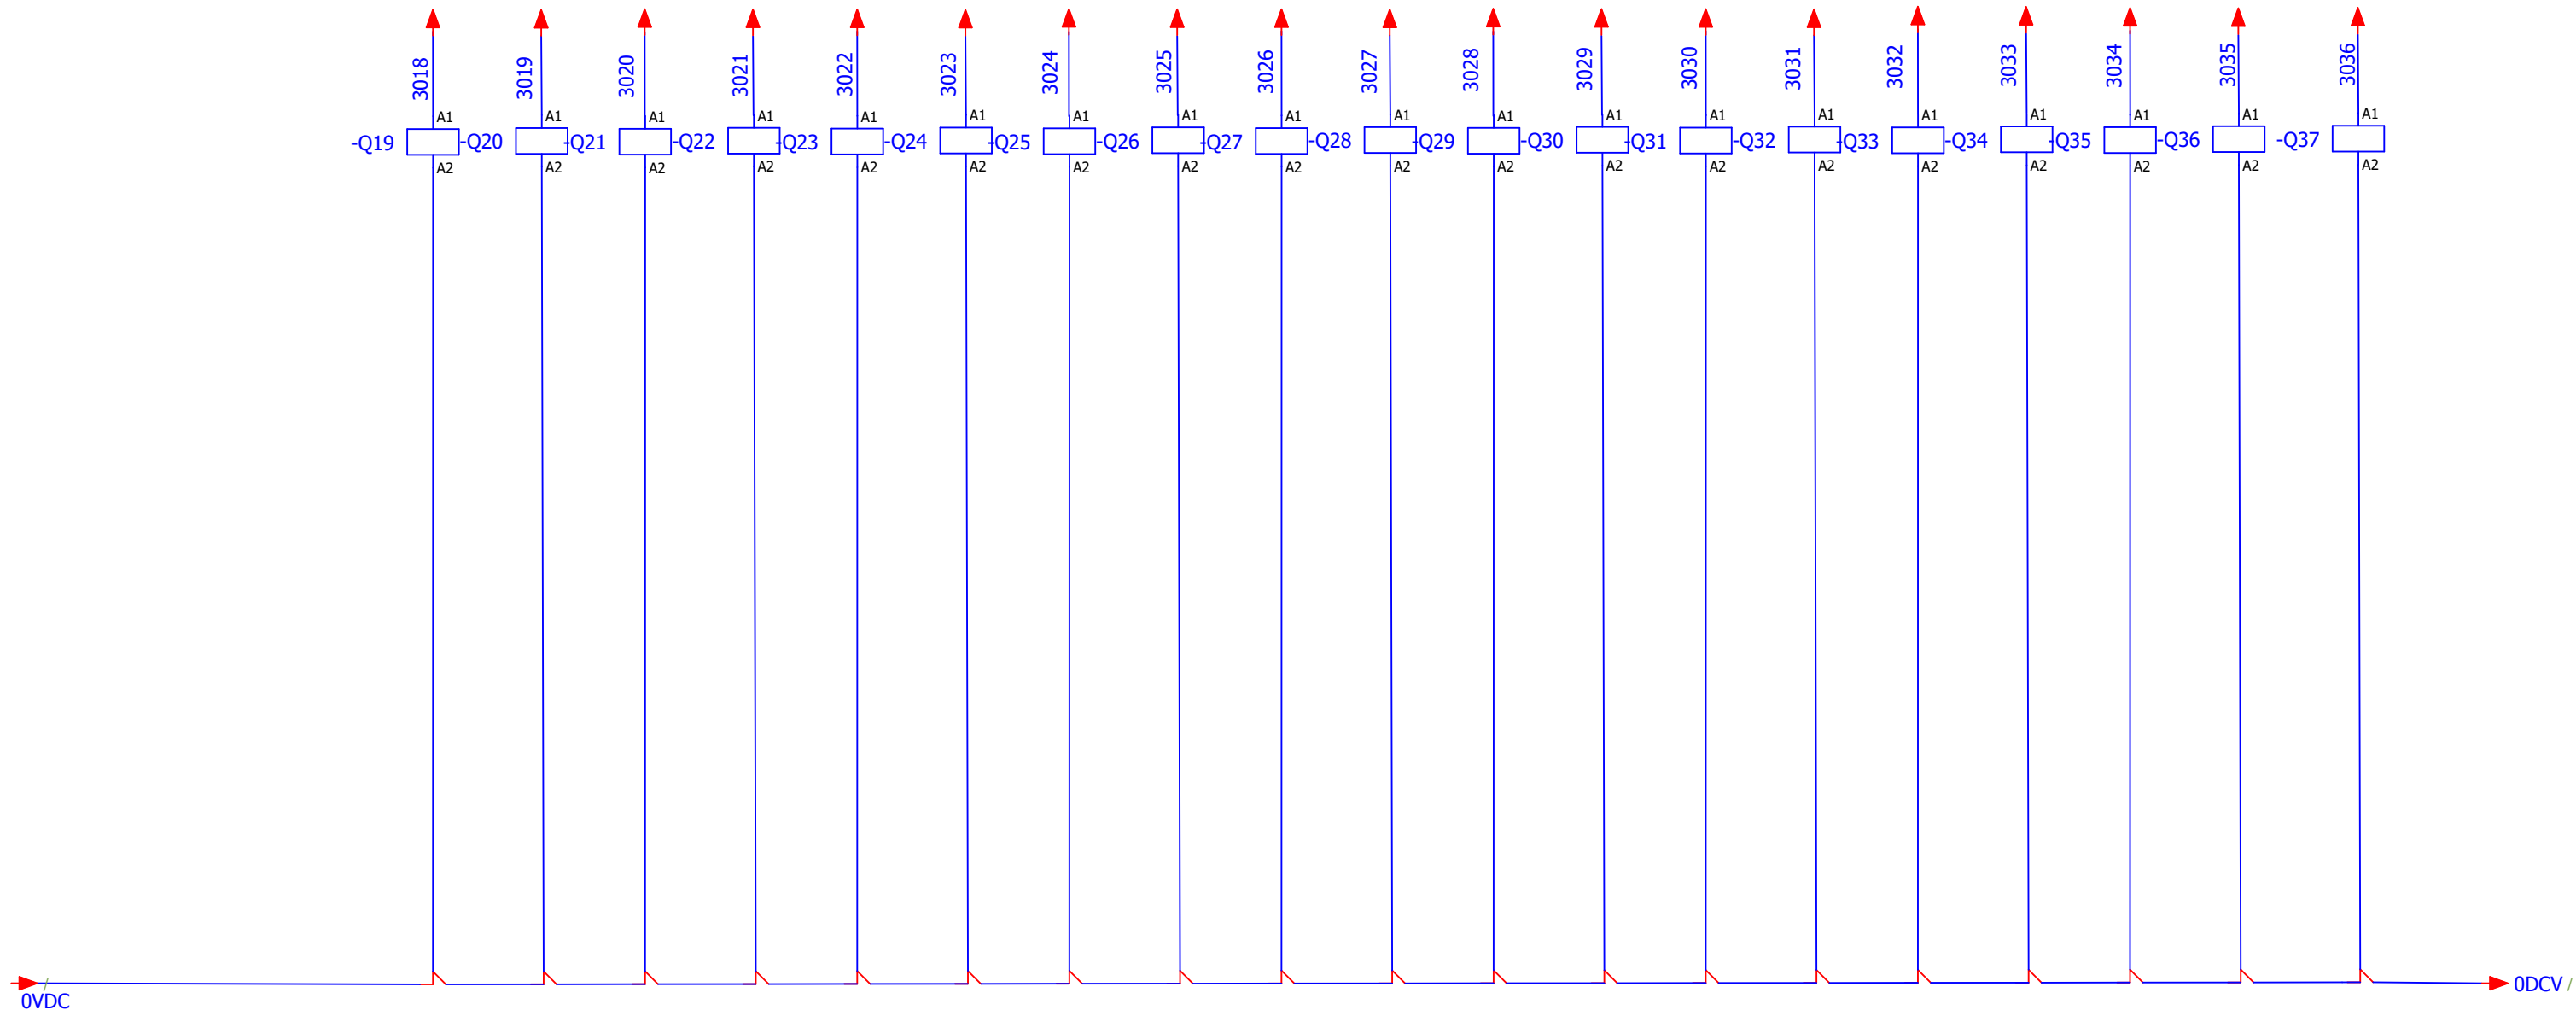



0	1	2	3	4	5	6	7	8	9
---	---	---	---	---	---	---	---	---	---

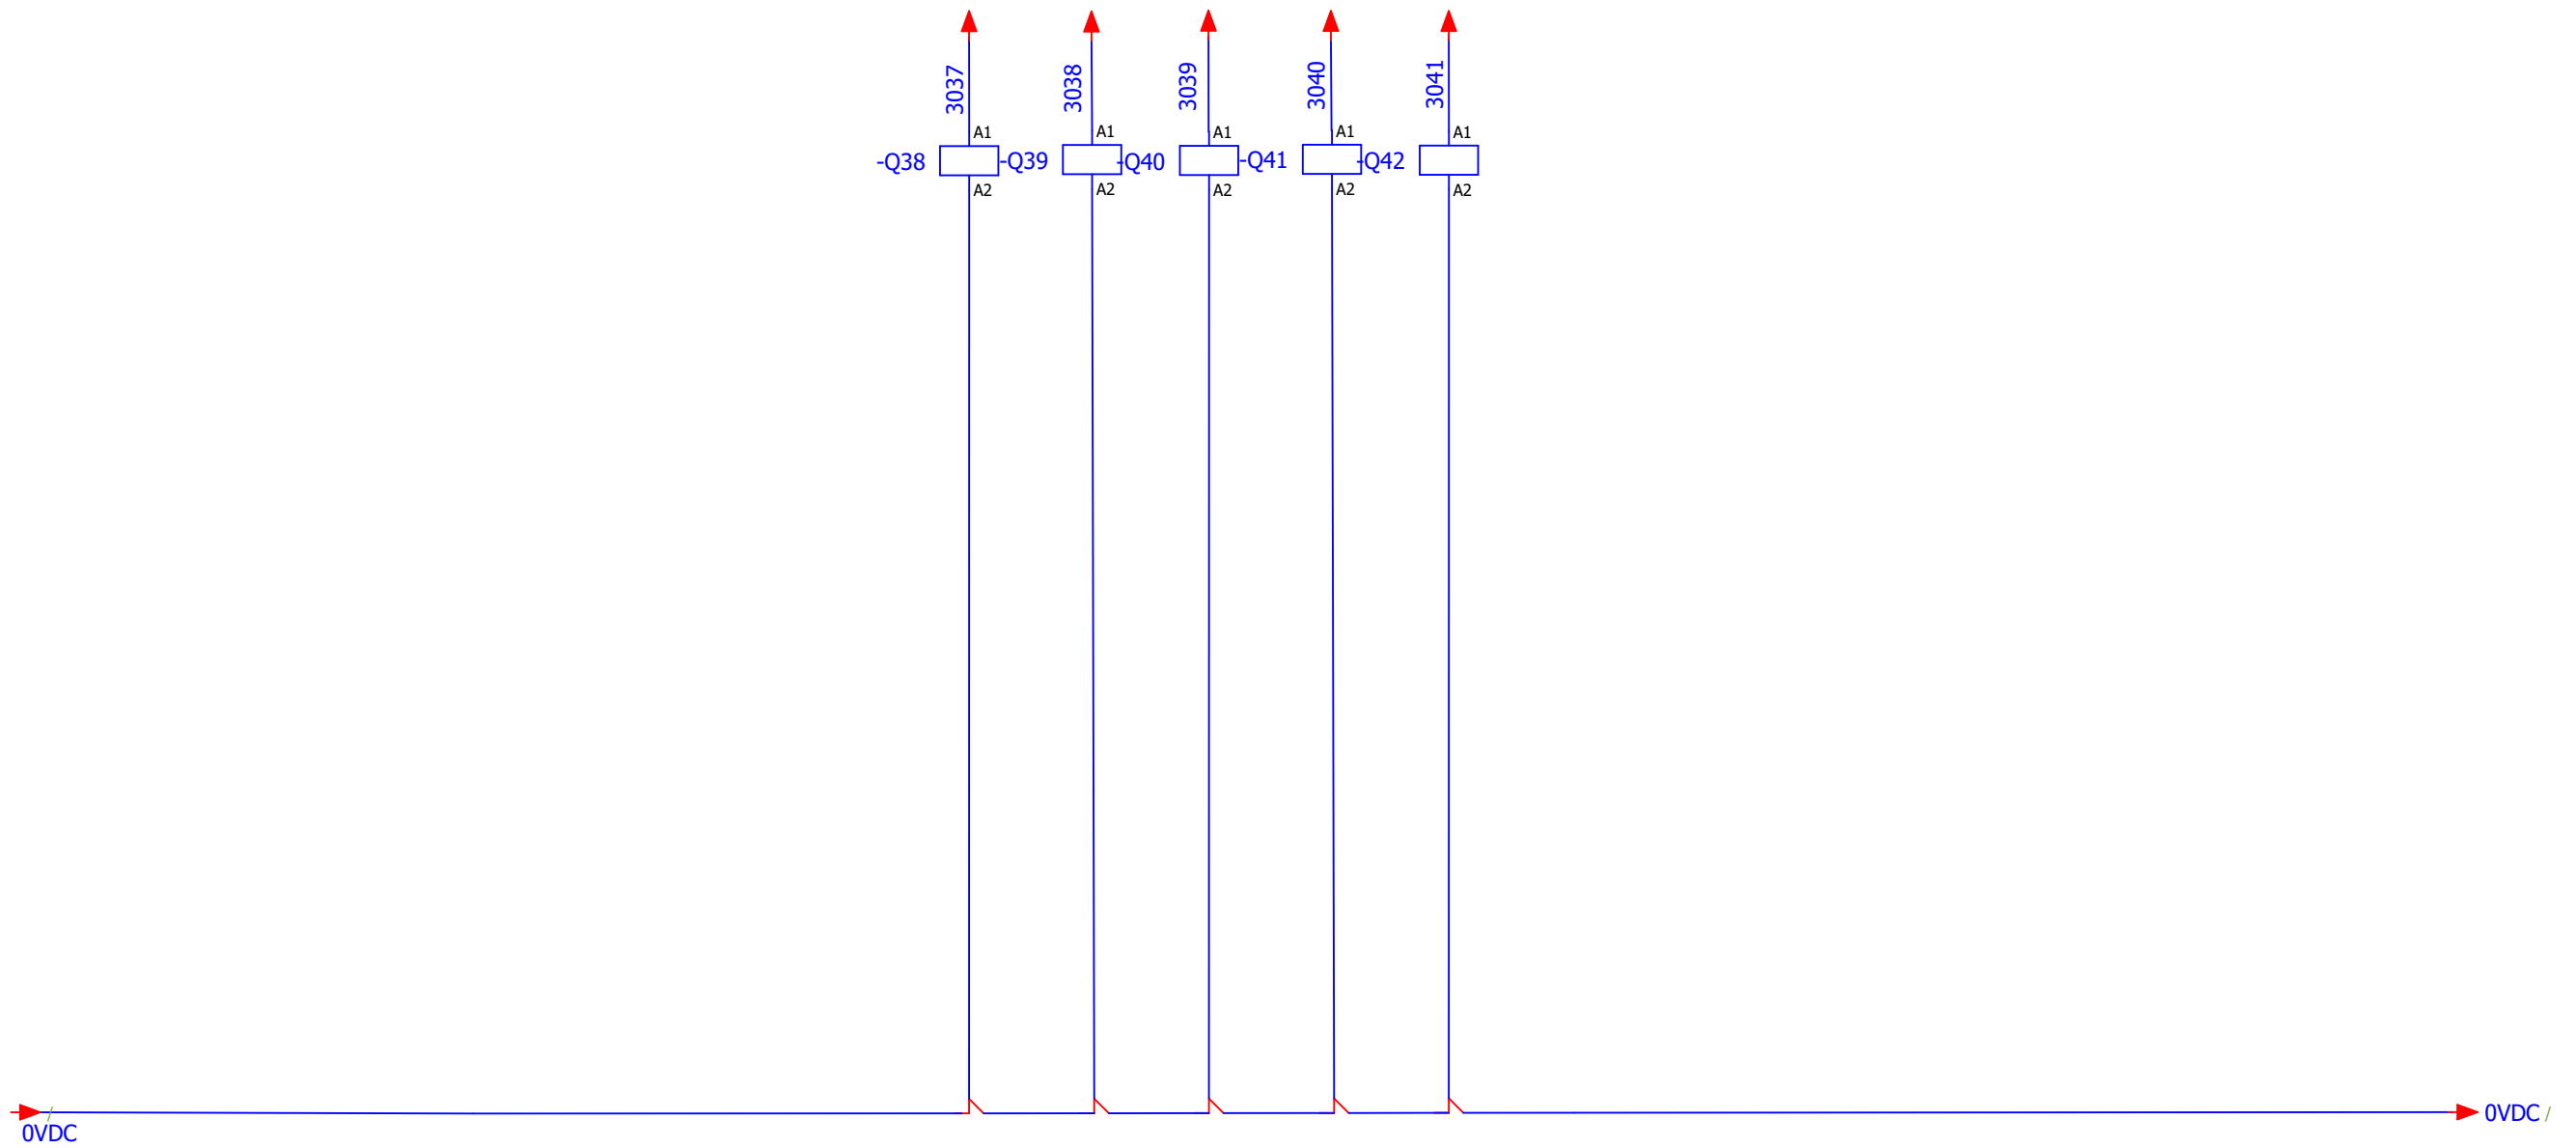


SİPARİŞ TARİHİ		 SRDR ROBOTİK TEL: +90 552 442 77 37 ADRES: Bağlarbaşı Mah. Yonca Sk. No:1 Kat:3/6 34844 Maltepe/İSTANBUL e-mail : info@srdrobotik.com	PROJE NO:		KONTROL EDEN İMZA:	EK AÇIKLAMA	12 RÖLE DAĞILIM SAYFASJ-3	
GÜNCELLEME TARİHİ	2.01.2023		KONTROL EDEN:				TOPLAM SAYFA SAYISI:	27
PROJE SORUMLUSU							ÖNCEKİ SAYFA:	11 RÖLE DAĞILIM SAYFASJ-2
MONTAJ SORUMLUSU							SONRAKİ SAYFA:	13 RÖLE KONTAK DAĞILIM SAYFASJ-4

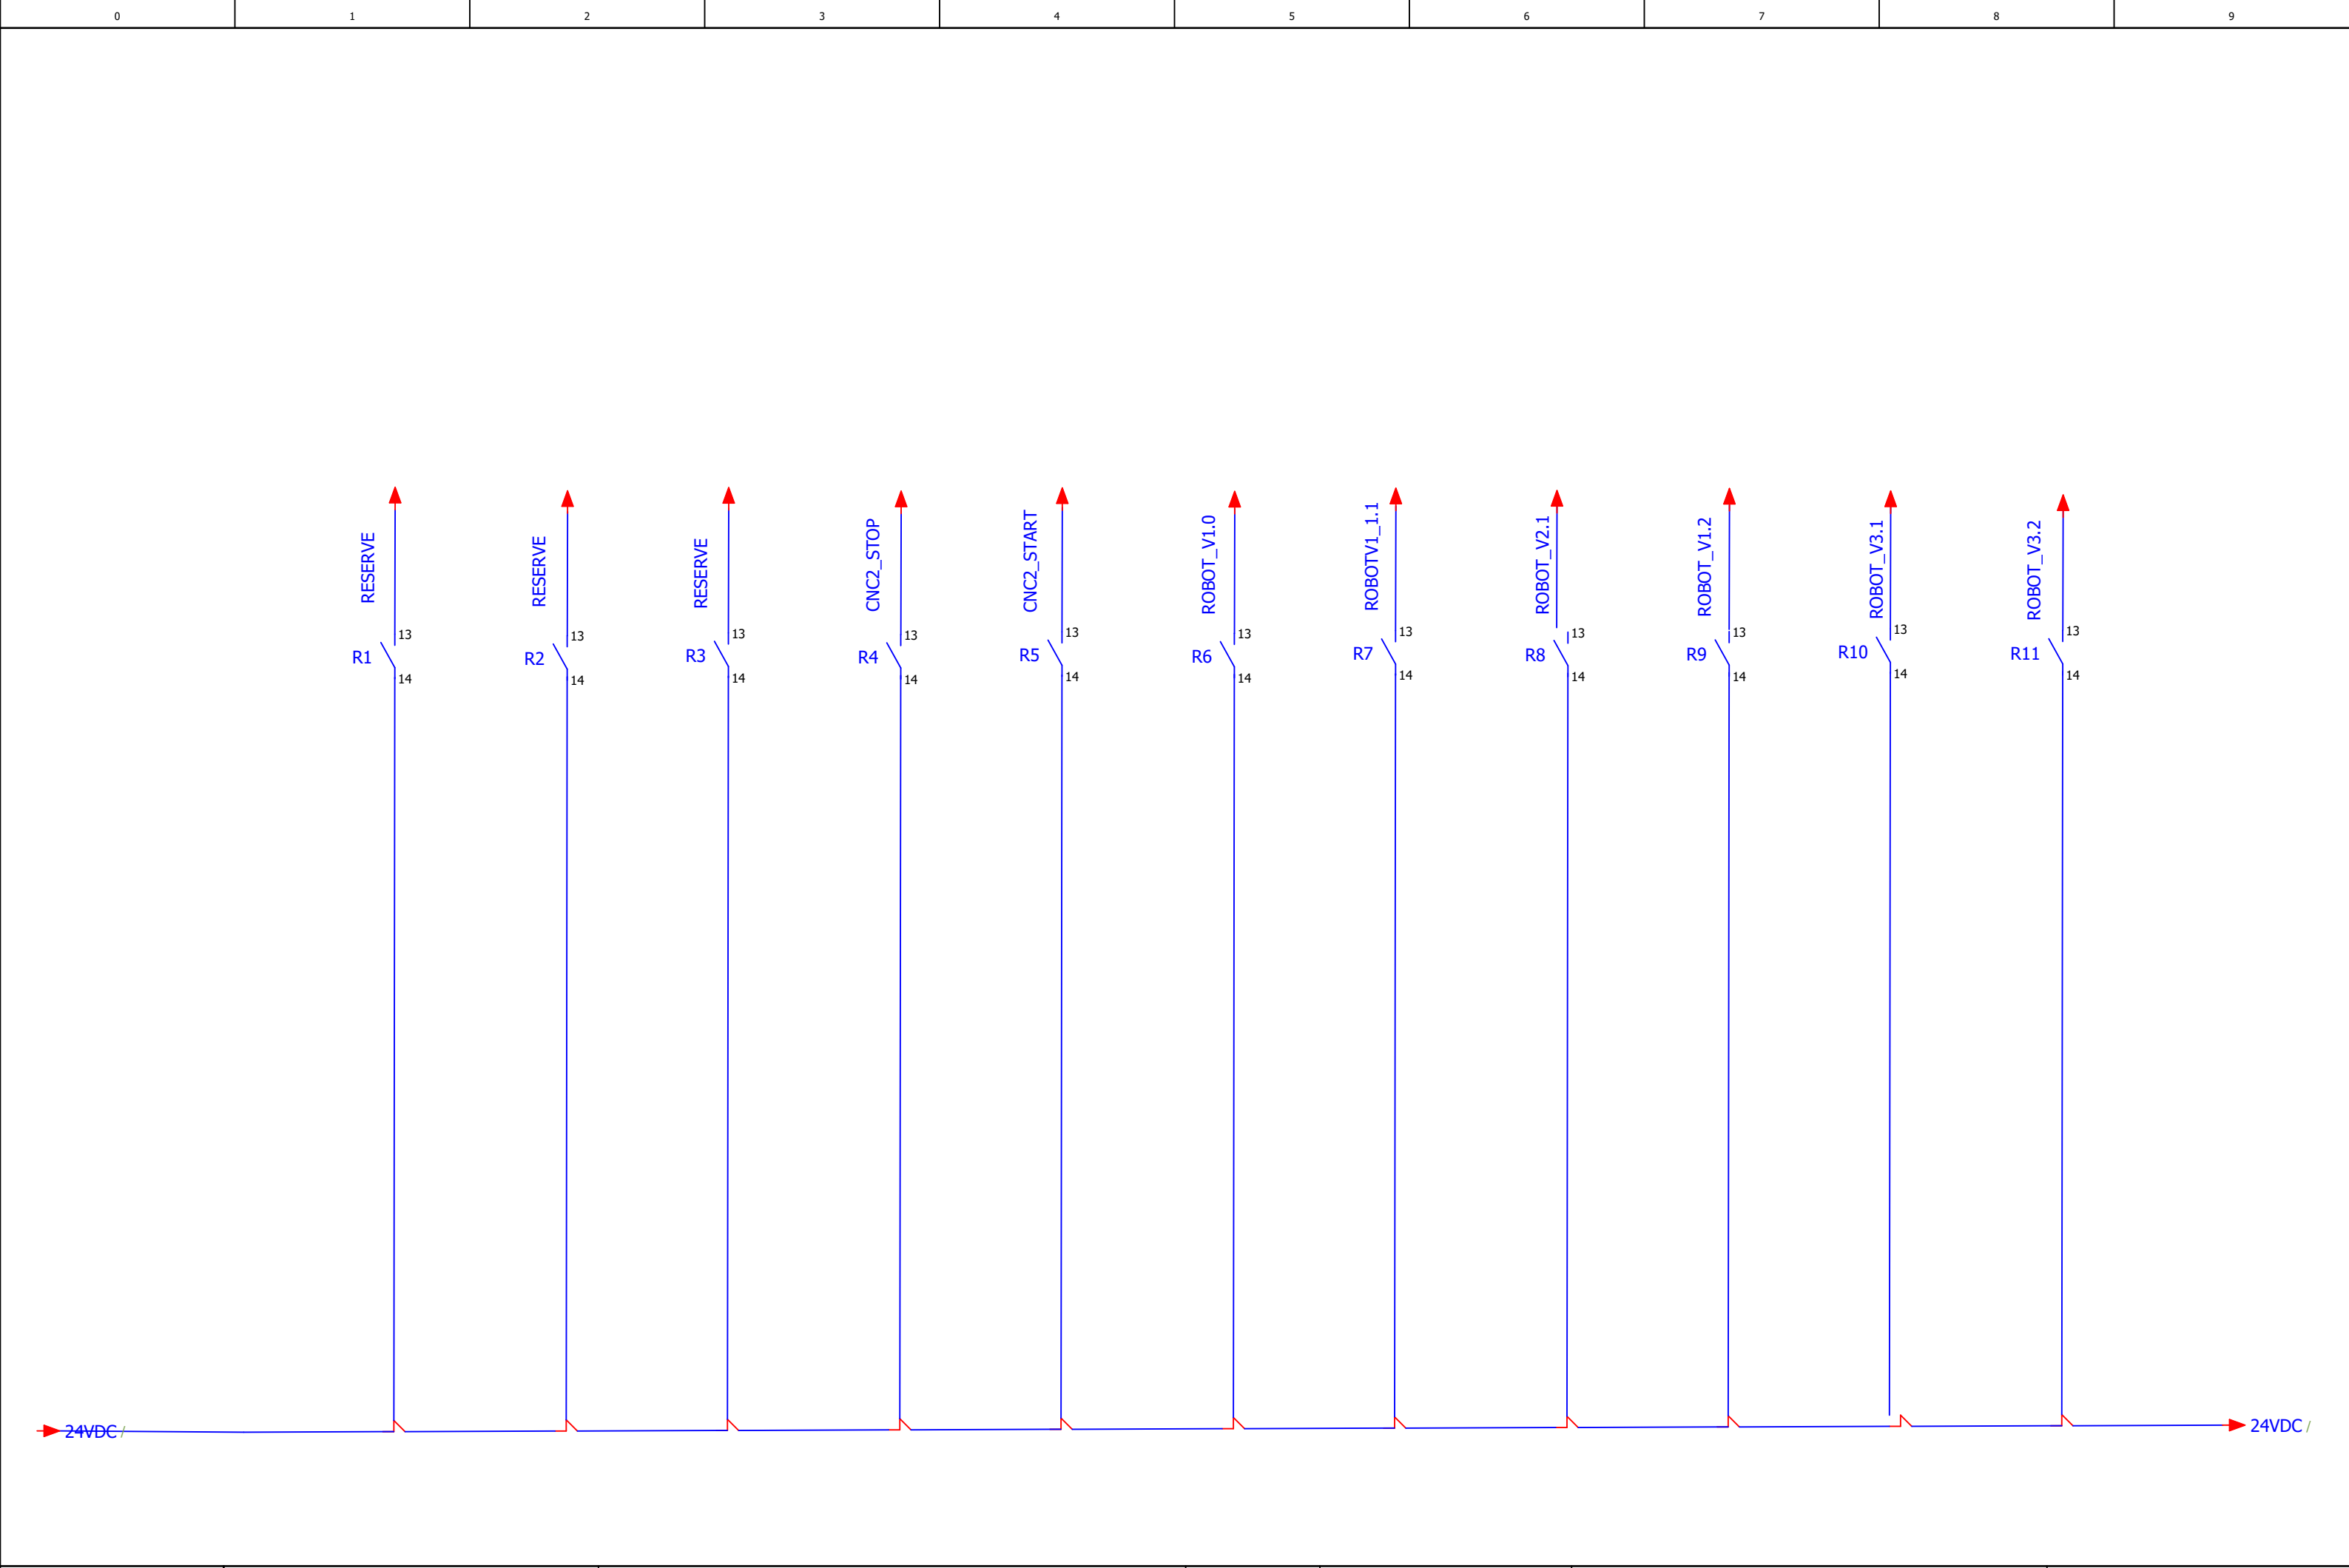


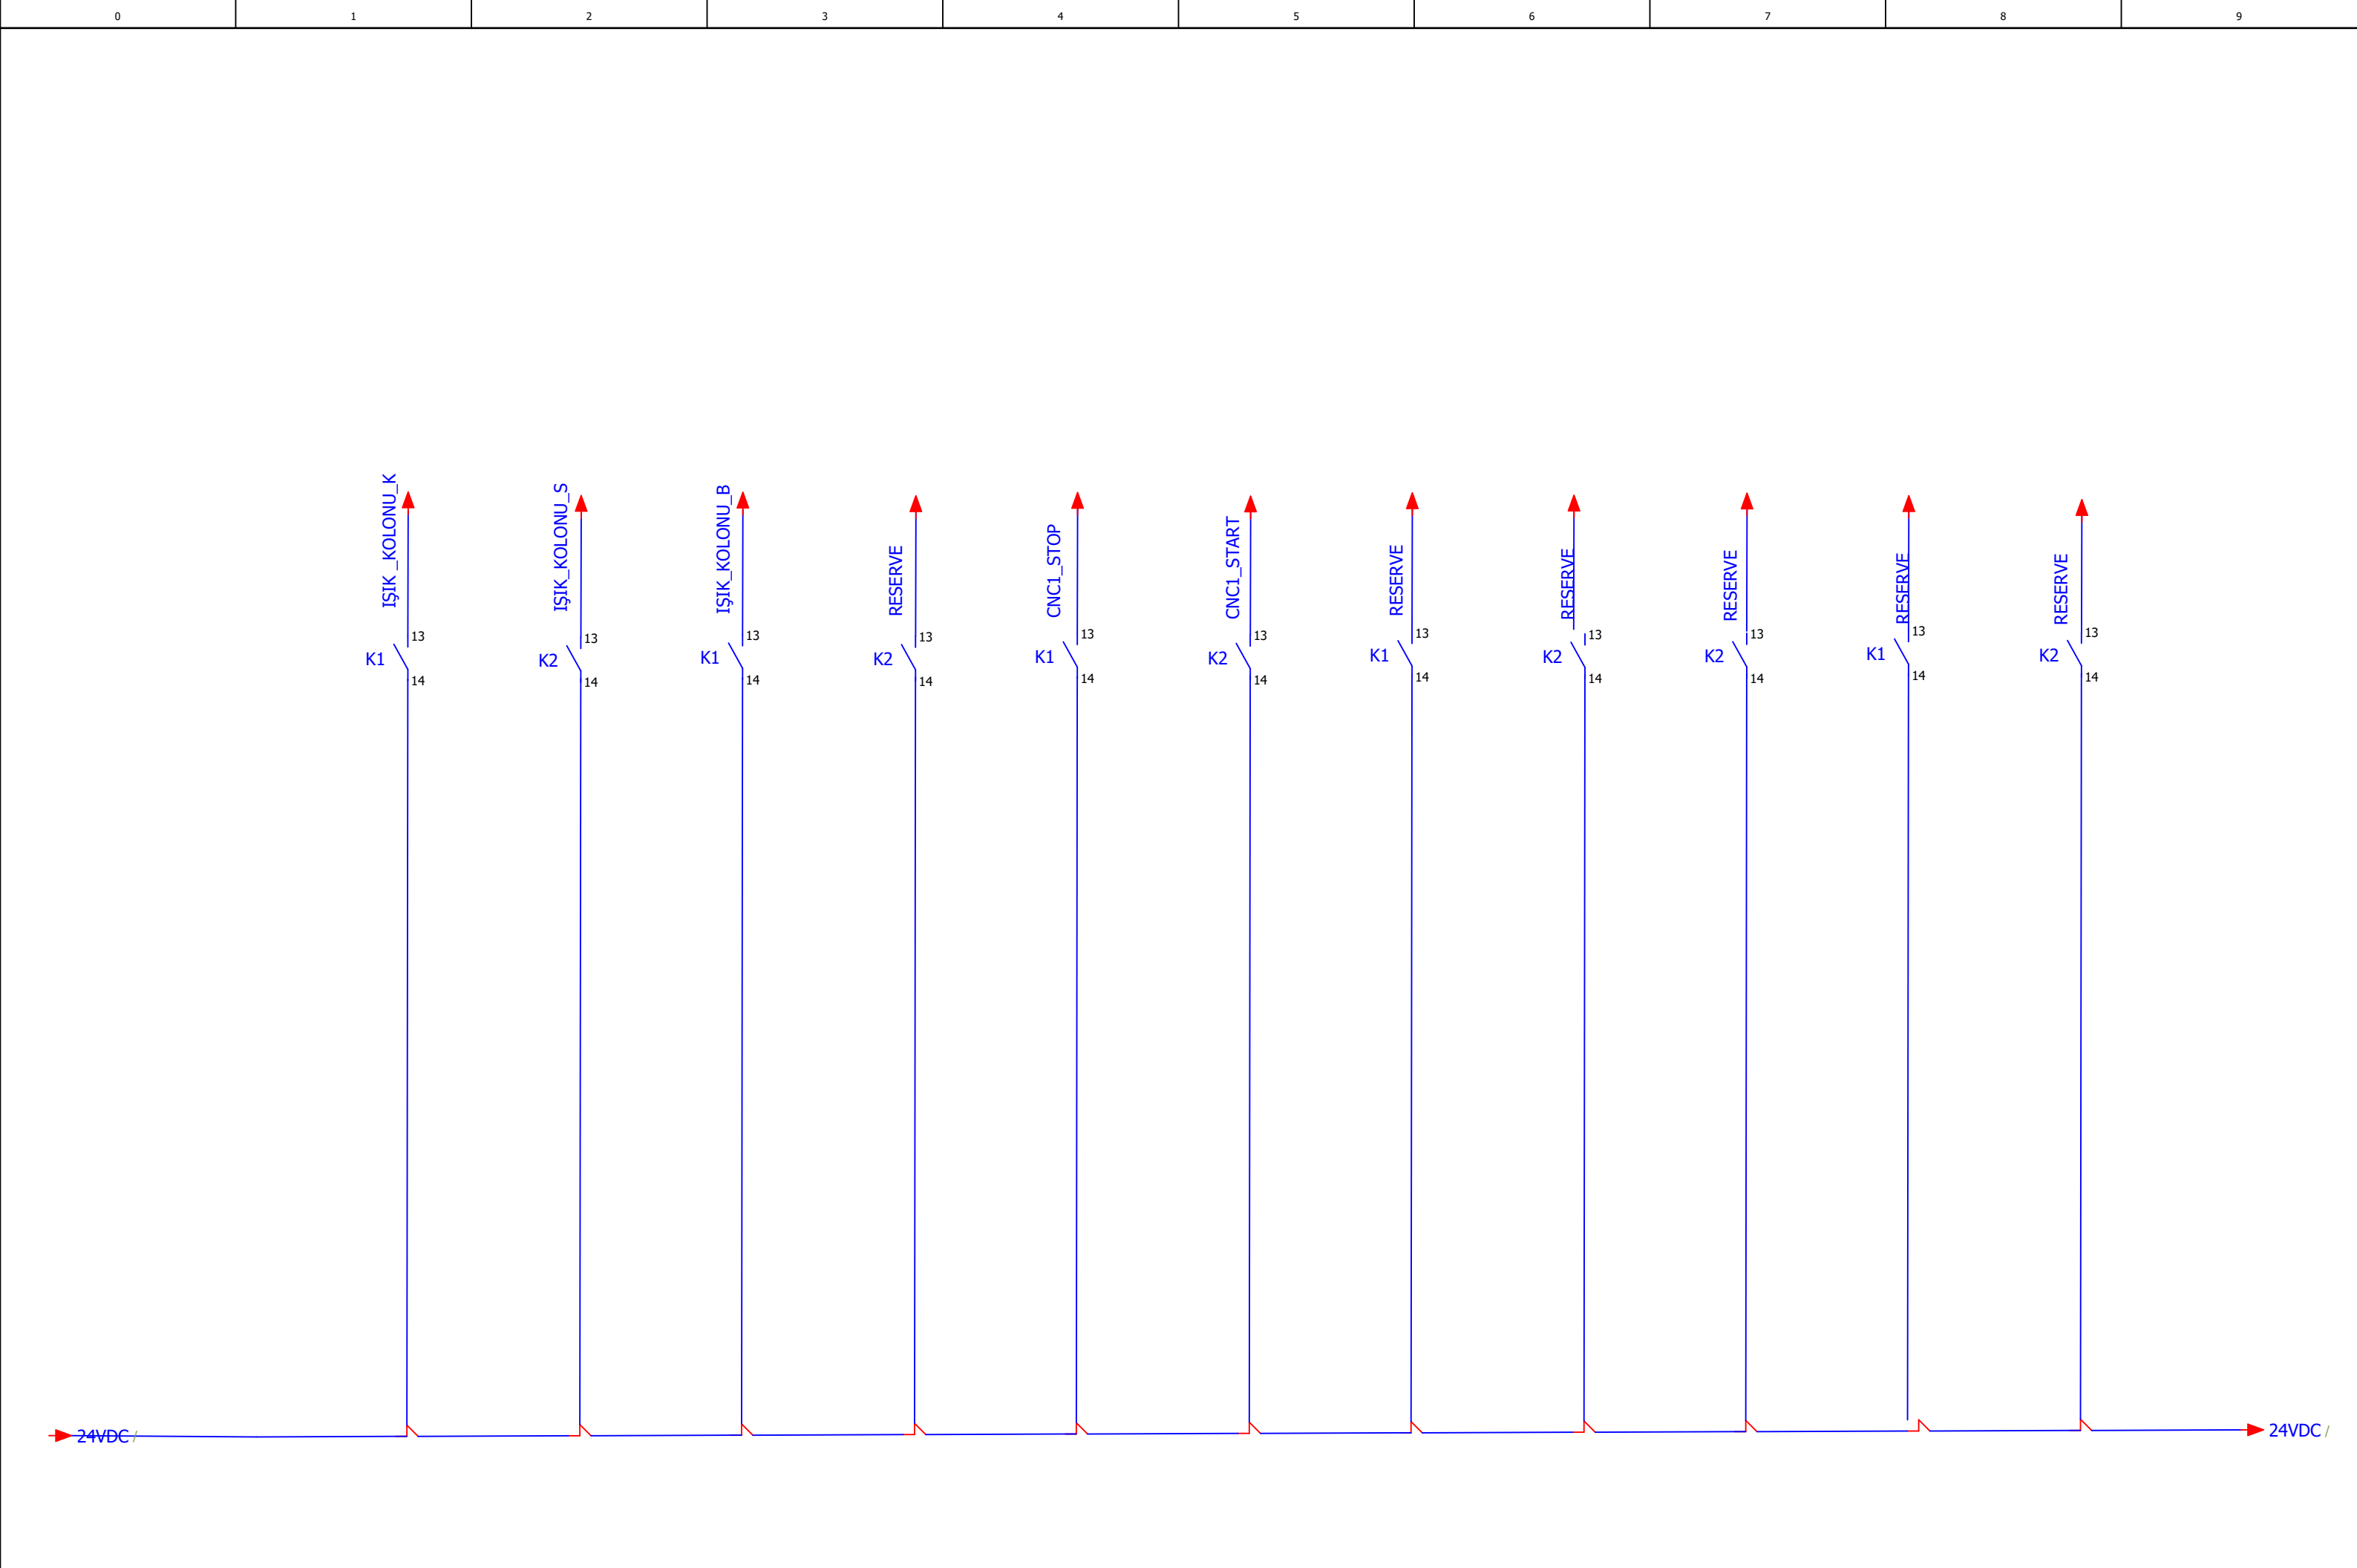

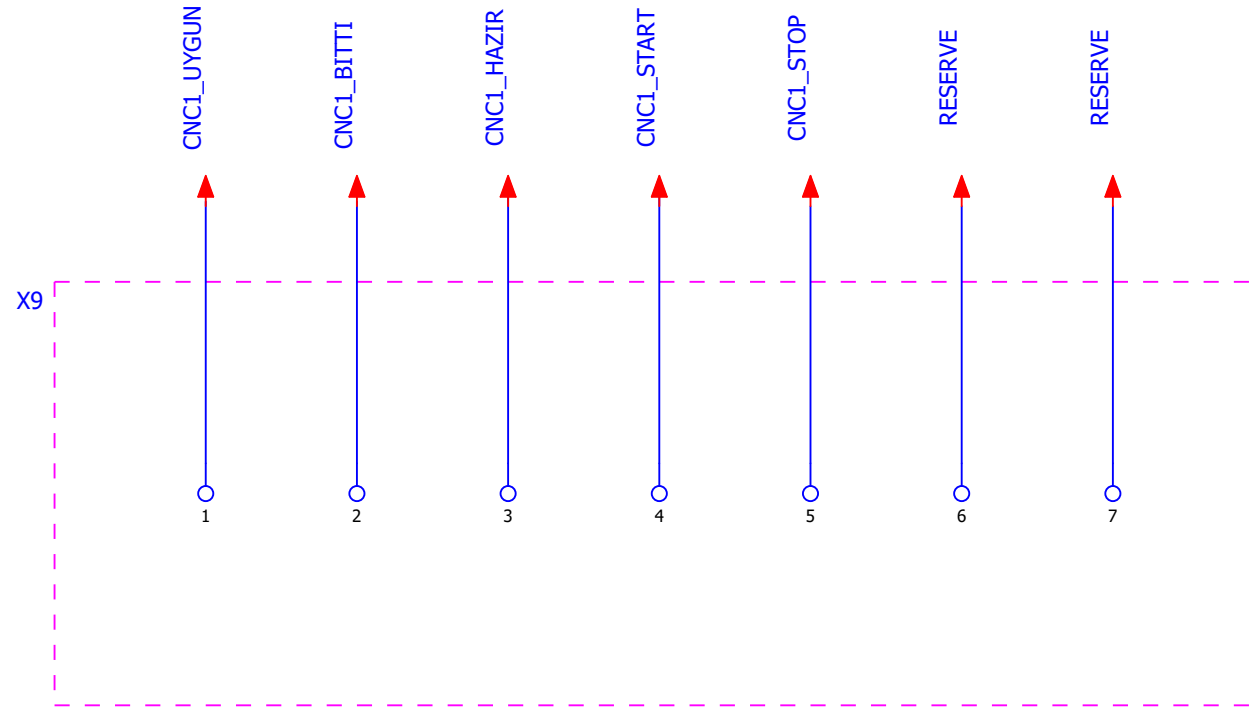



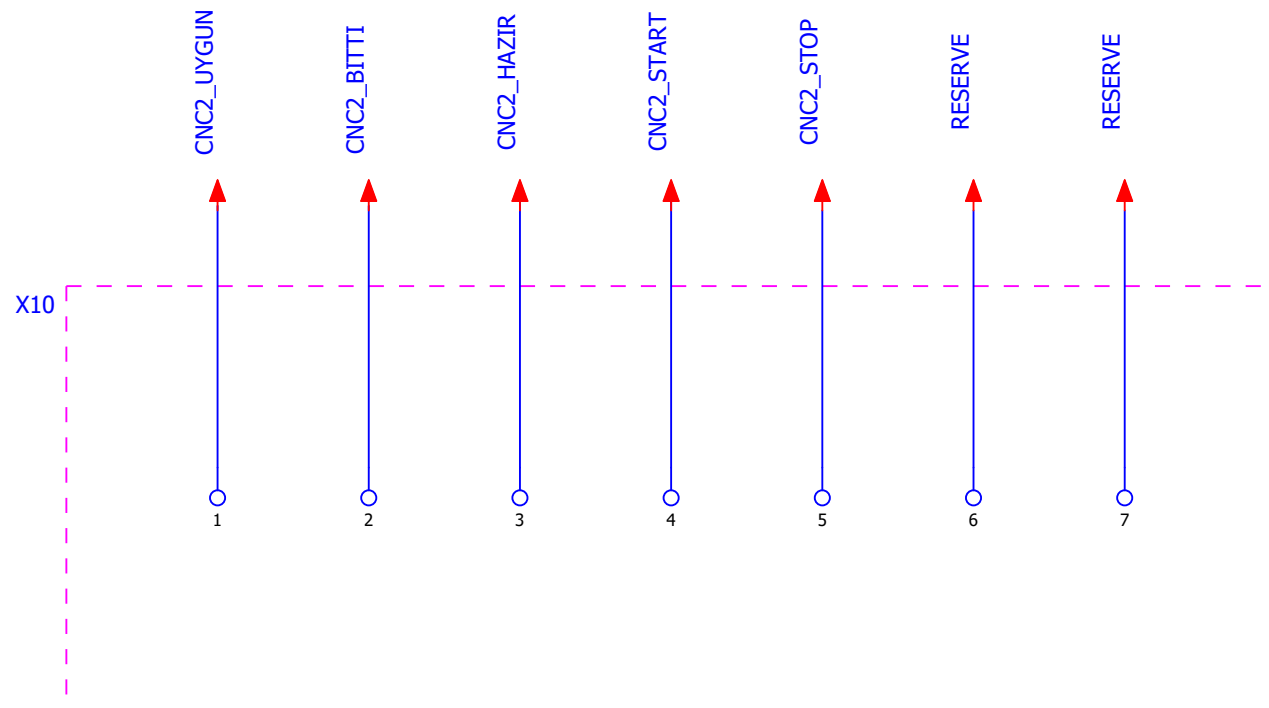



SİPARİŞ TARİHİ		 SRDR ROBOTİK TEL: +90 552 442 77 37 ADRES: Bağlarbaşı Mah. Yonca Sk. No:1 Kat:3/6 34844 Maltepe/İSTANBUL e-mail : info@srdrobotik.com	PROJE NO:		KONTROL EDEN İMZA:	EK AÇIKLAMA:	16	CNC2 HABERLEŞME TOPLAM SAYFA SAYISI: 27 ÖNCEKİ SAYFA: 15 CNC1 HABERLEŞME SONRAKİ SAYFA: 17 BUA-1 ROBOT BUA	
GÜNCELLEME TARİHİ	2.01.2023		KONTROL EDEN:						
PROJE SORUMLUSU									
MONTAJ SORUMLUSU									

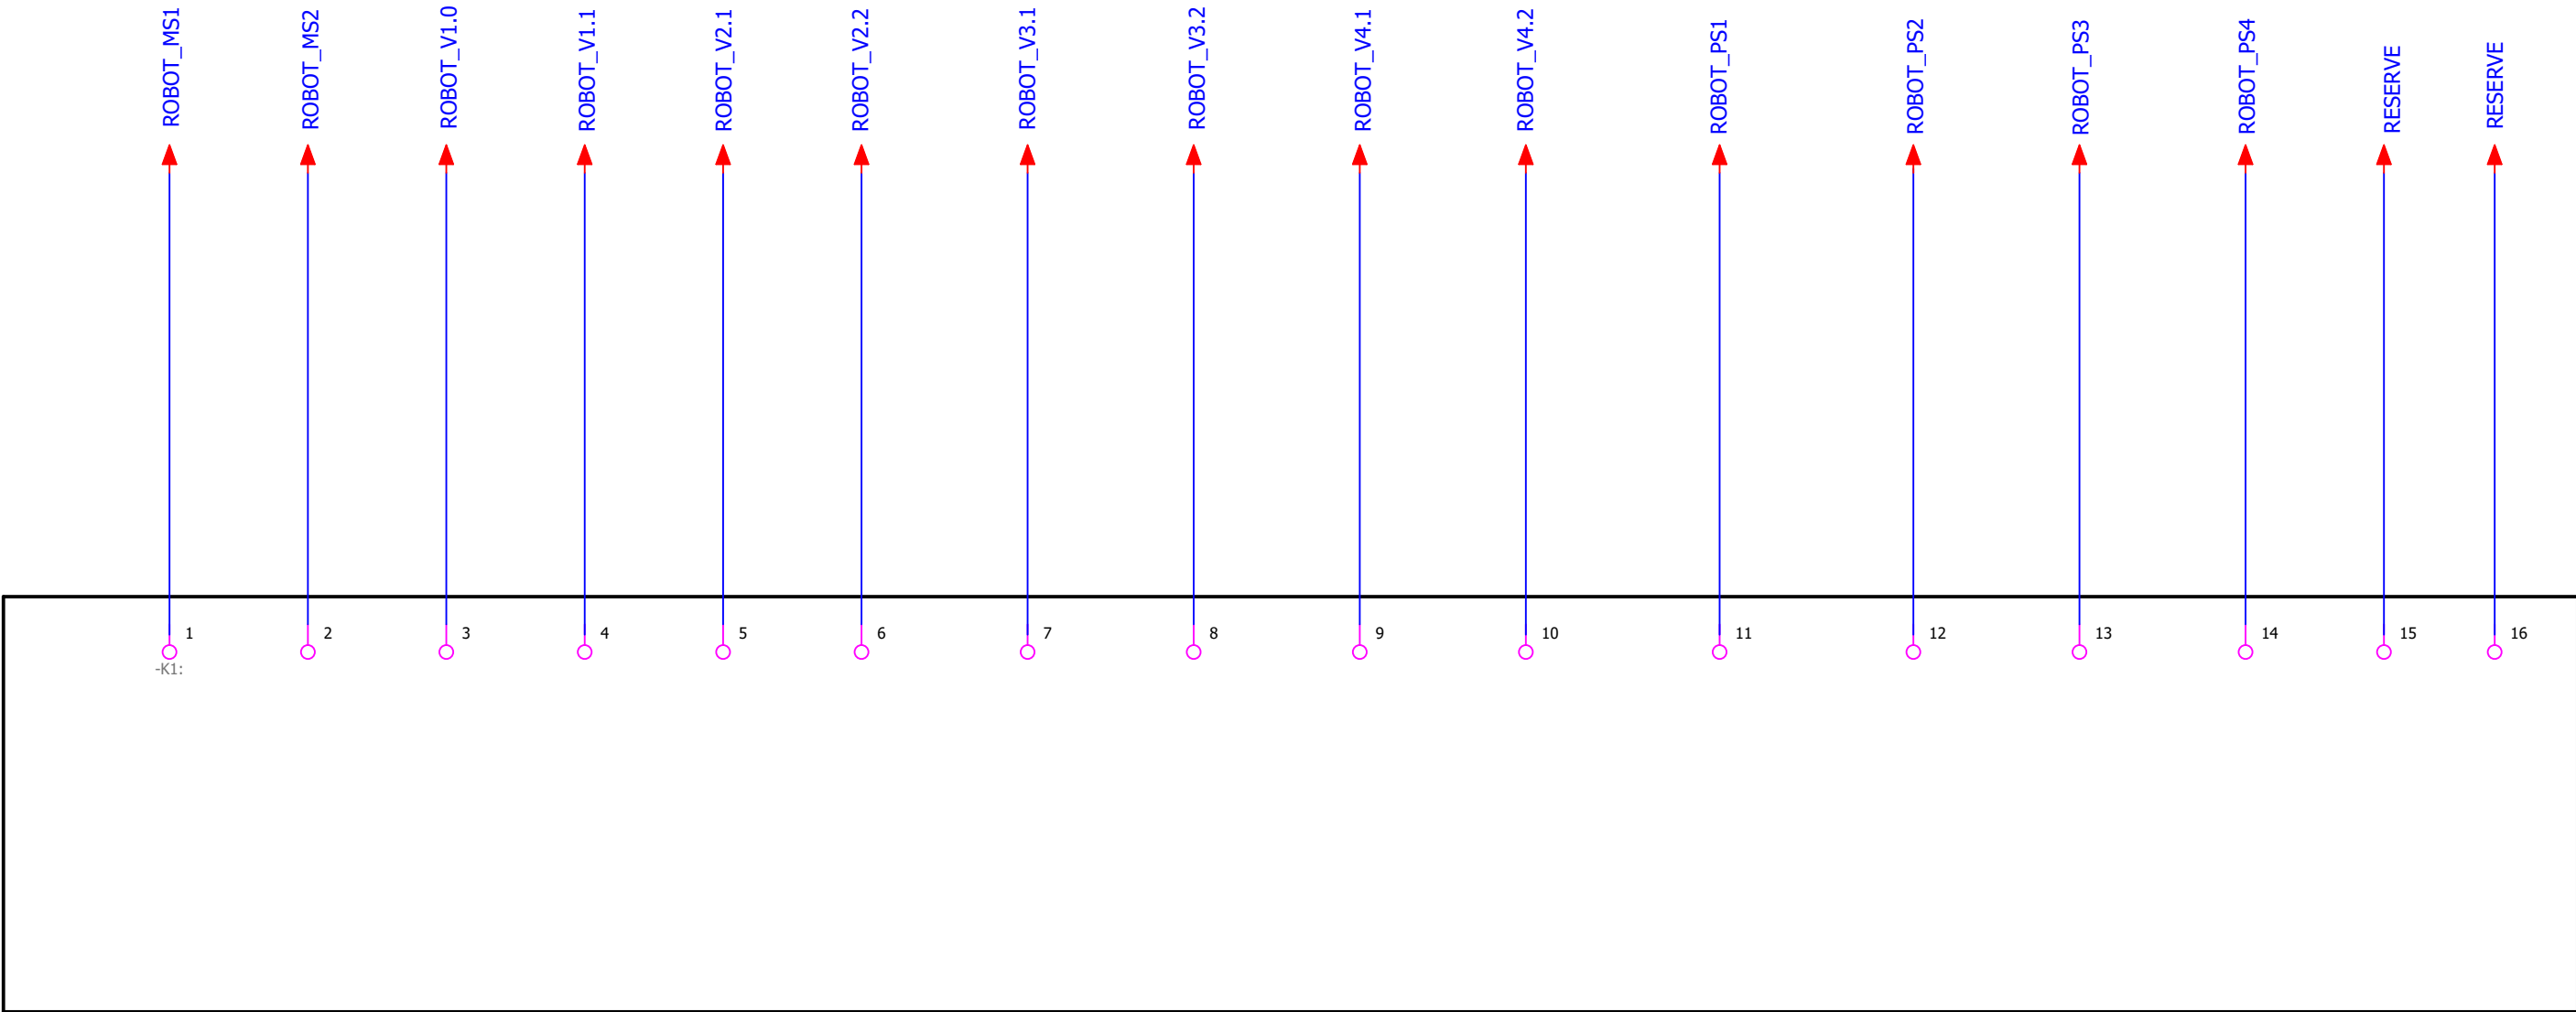

JB1

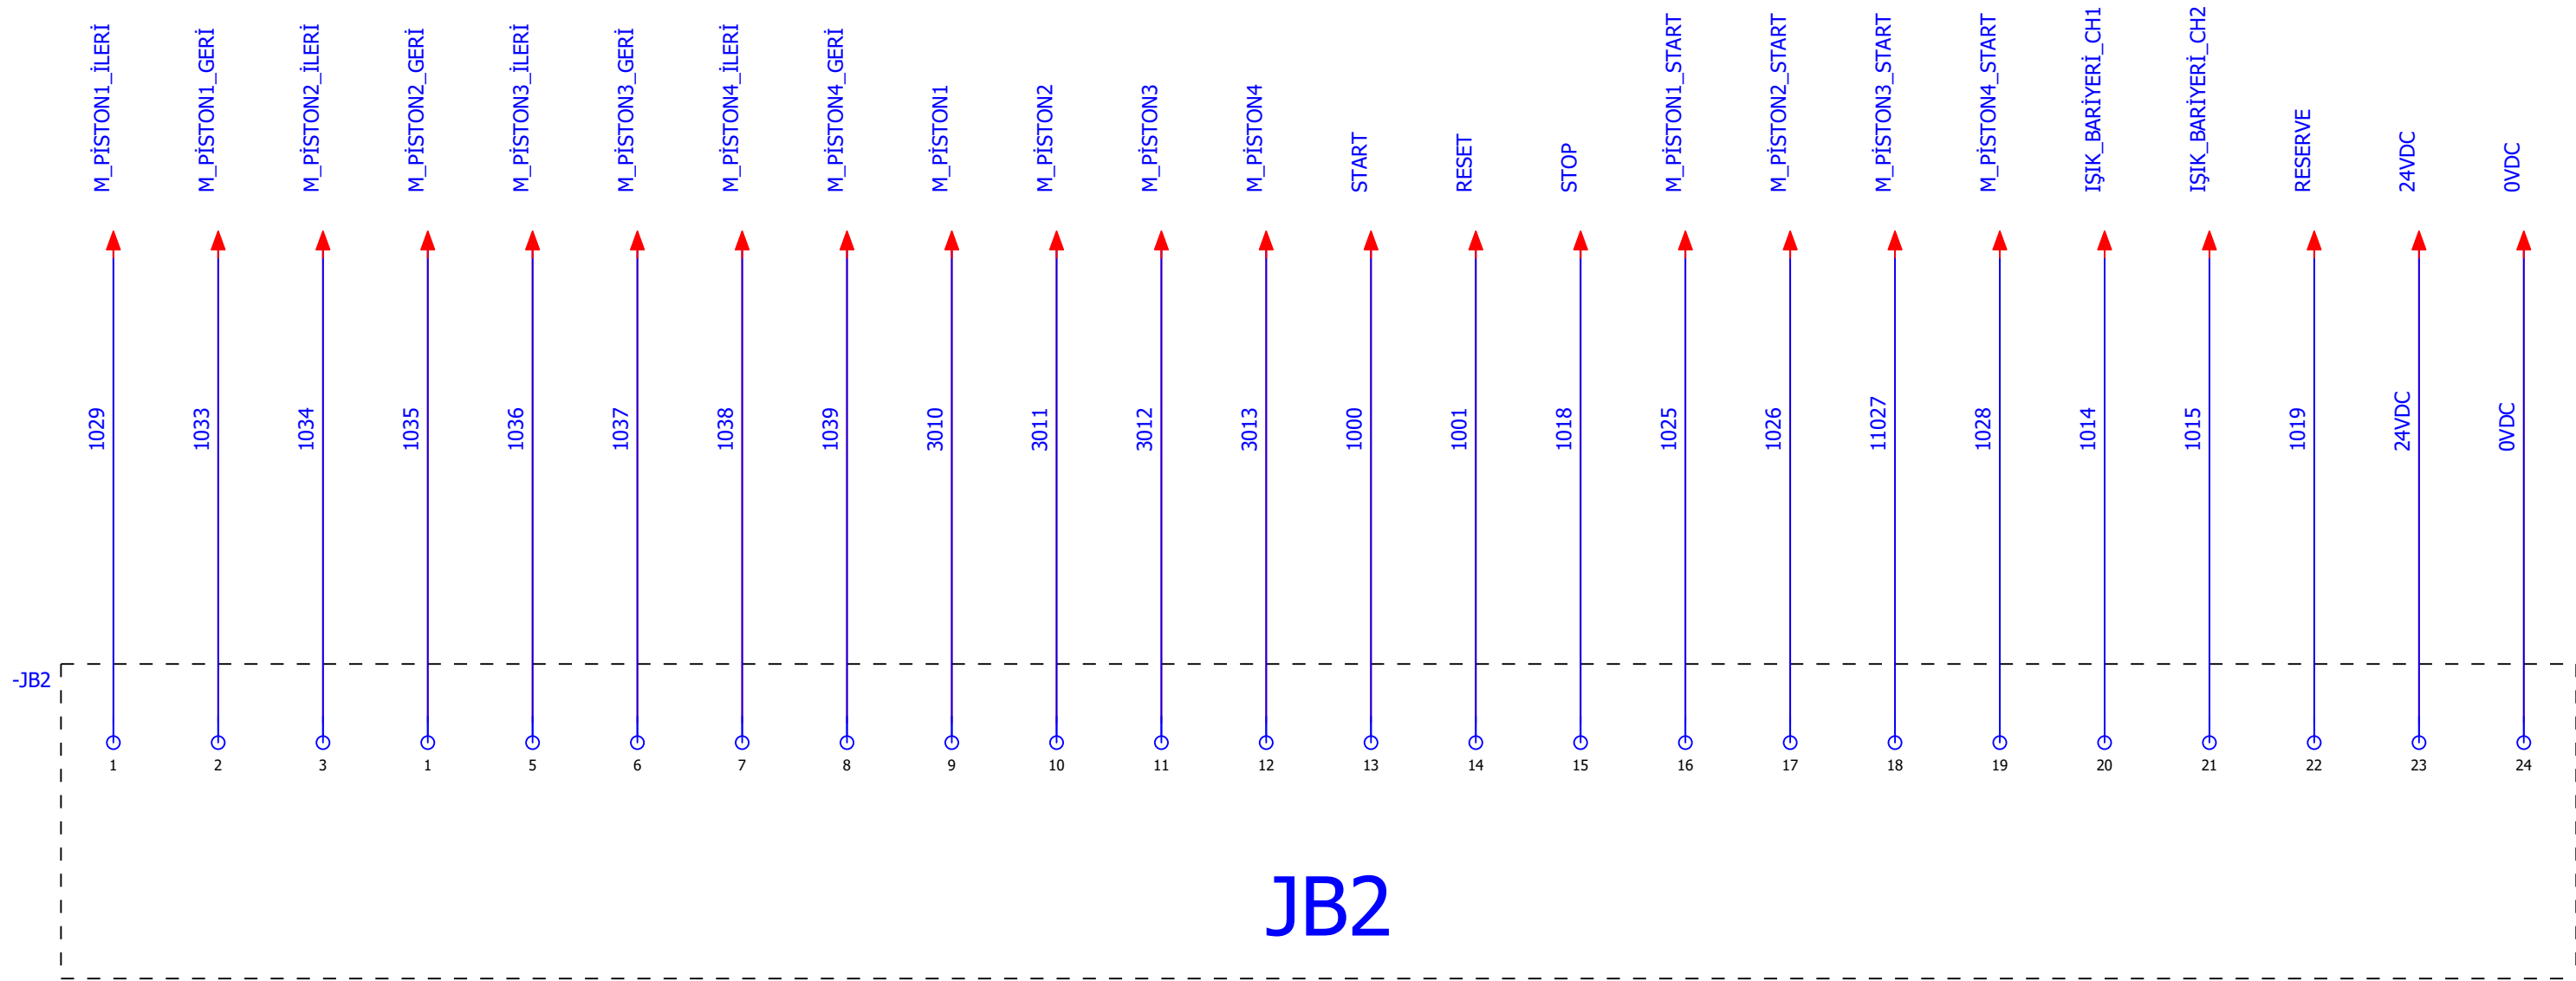

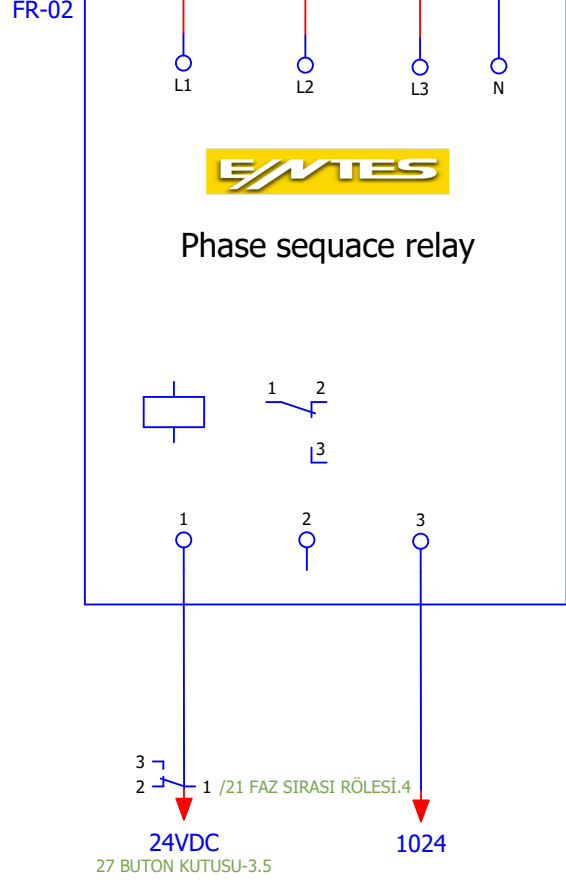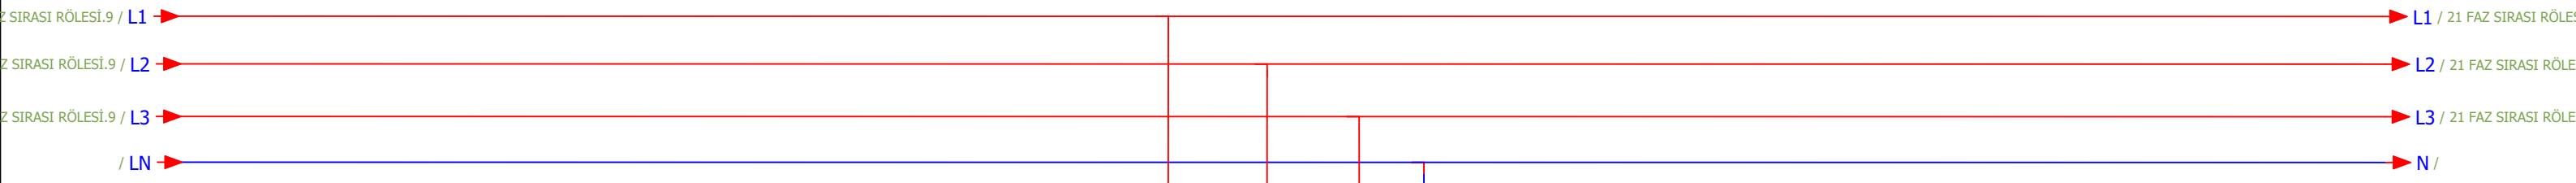

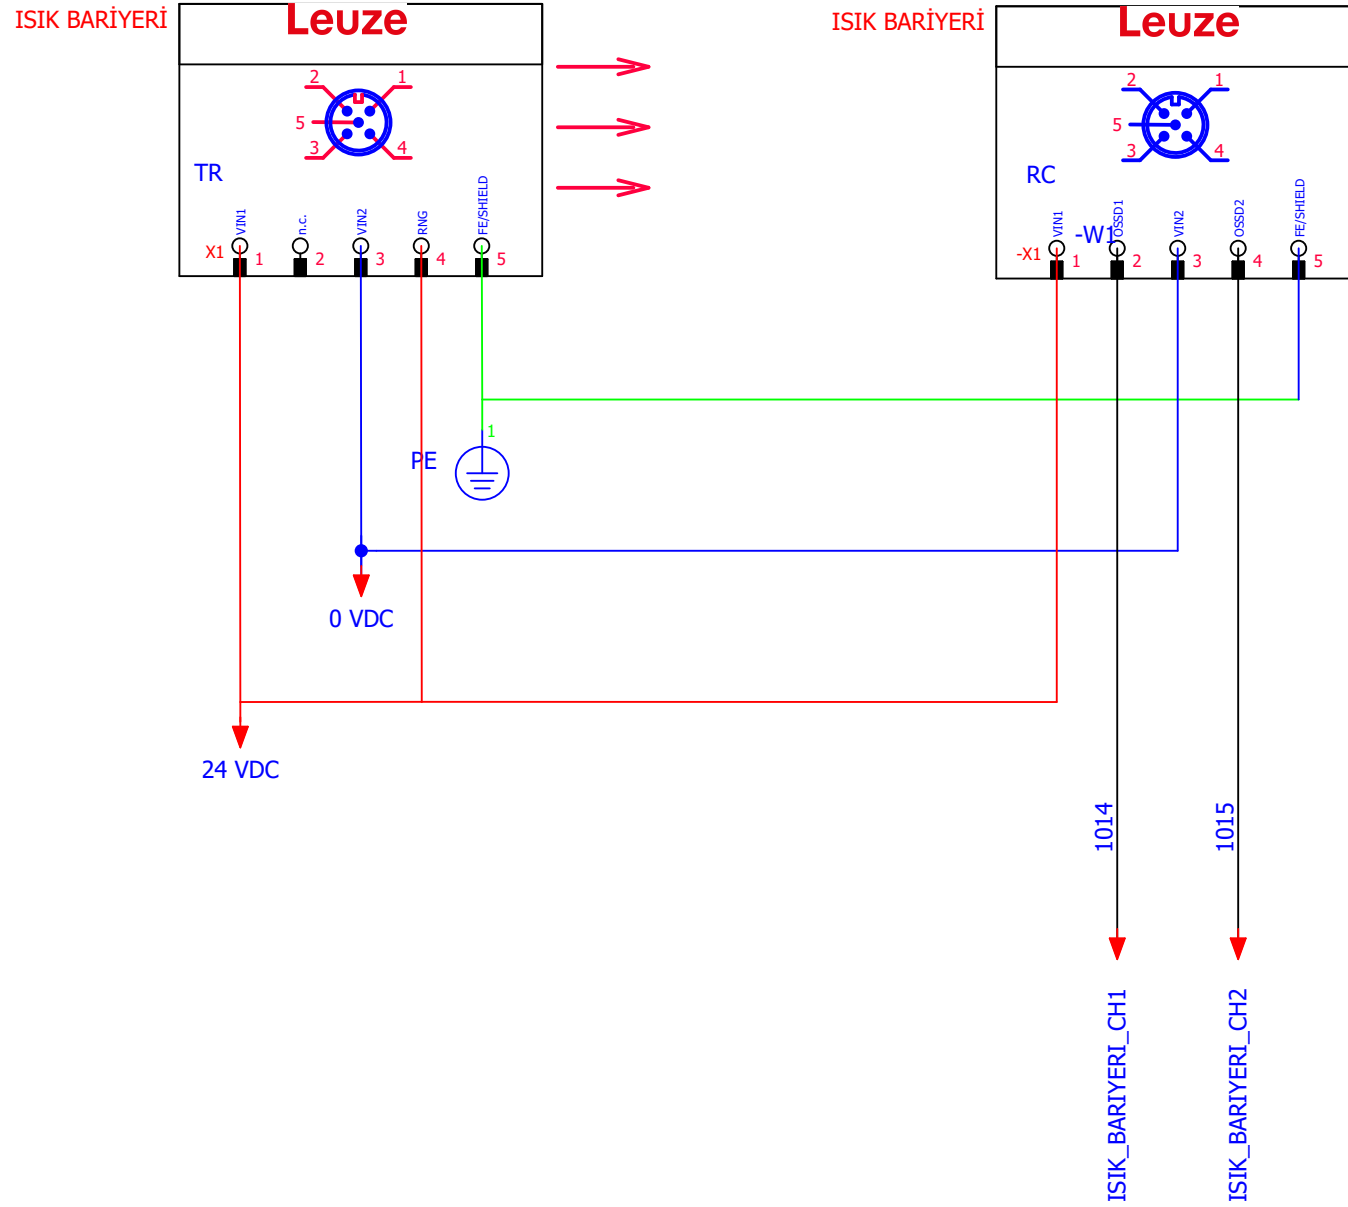



SIPARIŞ TARİHİ	
GÜNCELLEME TARİHİ	8.01.2023
PROJE SORUMLUSU	
MONTAJ SORUMLUSU	

 SRDR ROBOTİK TEL: +90 552 442 77 37 ADRES: Bağlarbaşı Mah. Yonca Sk. No:1 Kat:3/6 34844 Maltepe/İSTANBUL e-mail : info@srdrobotik.com

PROJE NO:	
KONTOL EDEN:	

KONTROL EDEN İMZA:	
EK AÇIKLAMA:	


22 ISIK BARIYERI	
TOPLAM SAYFA SAYISI:	27
ÖNCEKİ SAYFA:	21 FAZ SIRAŞI RÖLEŞİ
SÖNRAKİ SAYFA:	23 ISIK_KOLONU

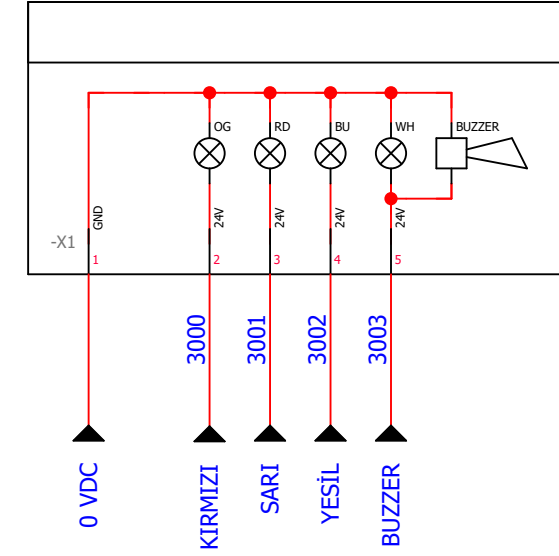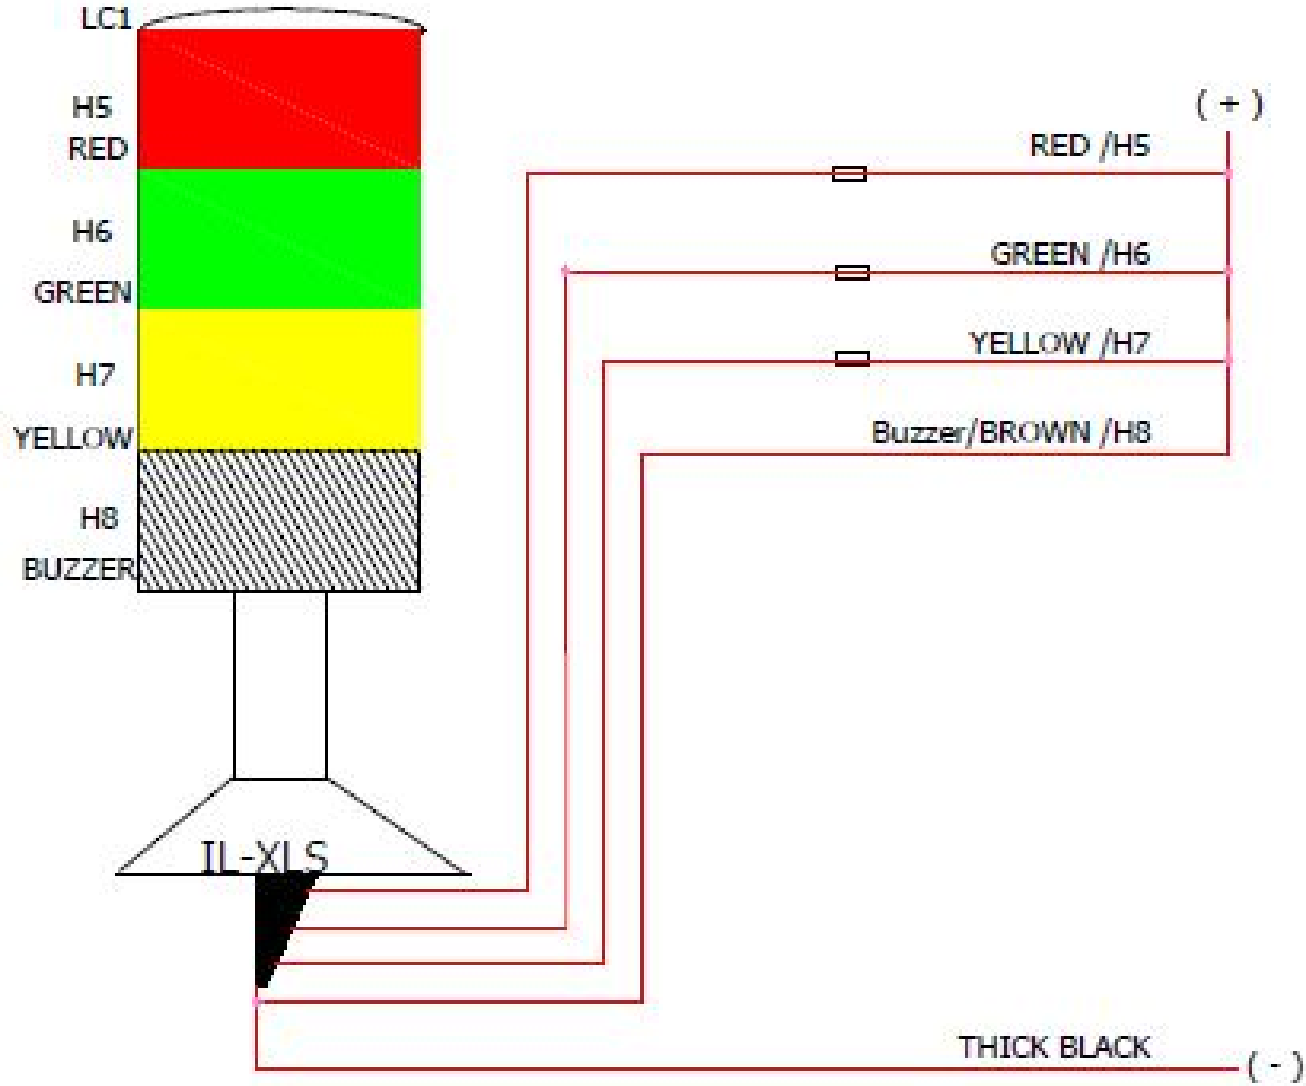

SİPARİŞ TARİHİ		 SRDR ROBOTİK TEL: +90 552 442 77 37 ADRES: Bağlarbaşı Mah. Yonca Sk. No:1 Kat:3/6 34844 Maltepe/İSTANBUL e-mail : info@srdrobotik.com	PROJE NO:		KONTROL EDEN İMZA:	EK AÇIKLAMA:	23 ISIK KOLONU	
GÜNCELLEME TARİHİ	8.01.2023		KONTROL EDEN:					
PROJE SORUMLUSU							TOPLAM SAYFA SAYISI:	27
MONTAJ SORUMLUSU							ÖNCEKİ SAYFA:	22 ISIK_BARIYERİ
							SONRAKİ SAYFA:	24 KAPI_SWITCH



KS1
EUCHNER KAPI SWITCH

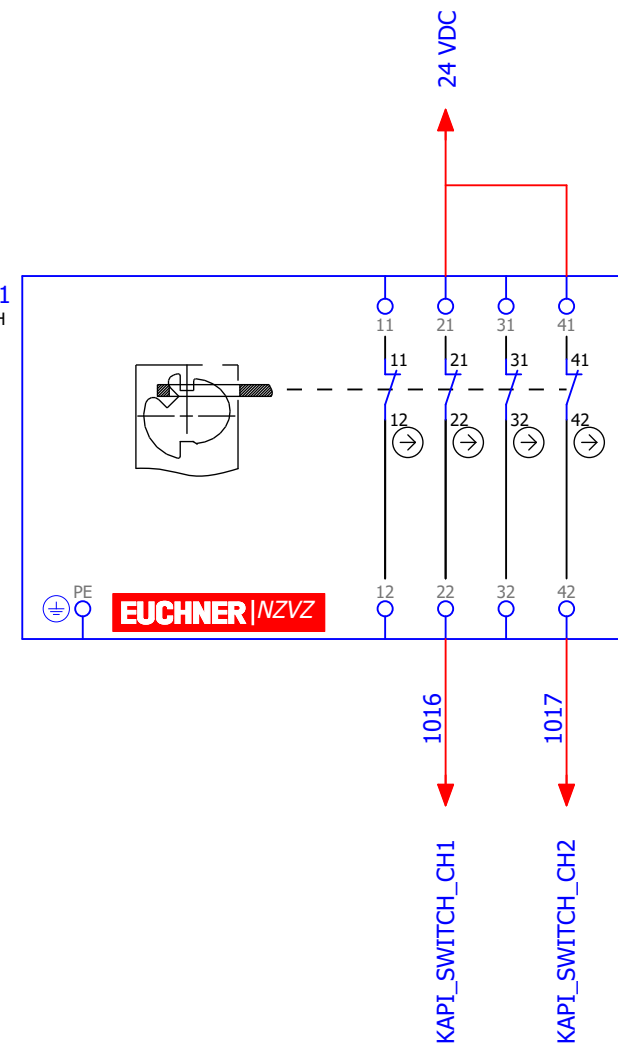



SİPARİŞ TARİHİ	
GÜNCELLEME TARİHİ	8.01.2023
PROJE SORUMLUSU	
MONTAJ SORUMLUSU	

	SRDR ROBOTİK TEL: +90 552 442 77 37 ADRES: Bağlarbaşı Mah. Yonca Sk. No:1 Kat:3/6 34844 Maltepe/İSTANBUL e-mail : info@srdrobotik.com
---	--

PROJE NO:	
KONTOL EDEN:	

KONTROL EDEN İMZA:	EK AÇIKLAMA:
--------------------	--------------

24 KAPI_SWITCH	
TOPLAM SAYFA SAYISI:	27
ÖNCEKİ SAYFA:	23 İSİK_KOLONU
SÖNRAKİ SAYFA:	25 BUTON_KUTUSU

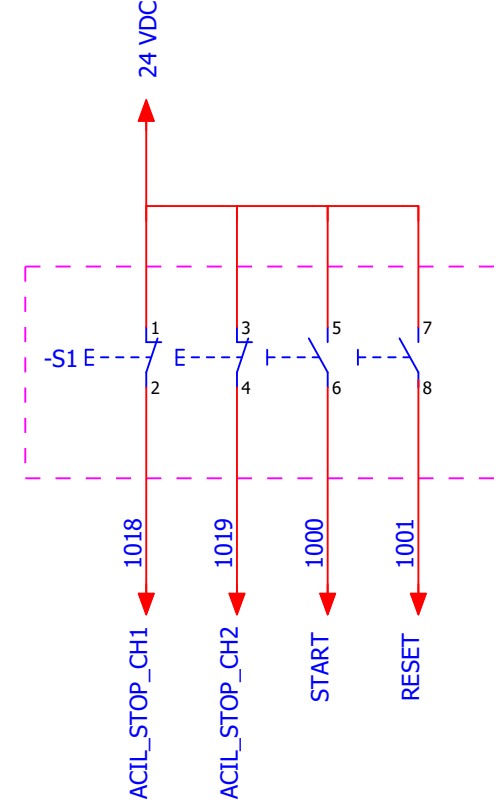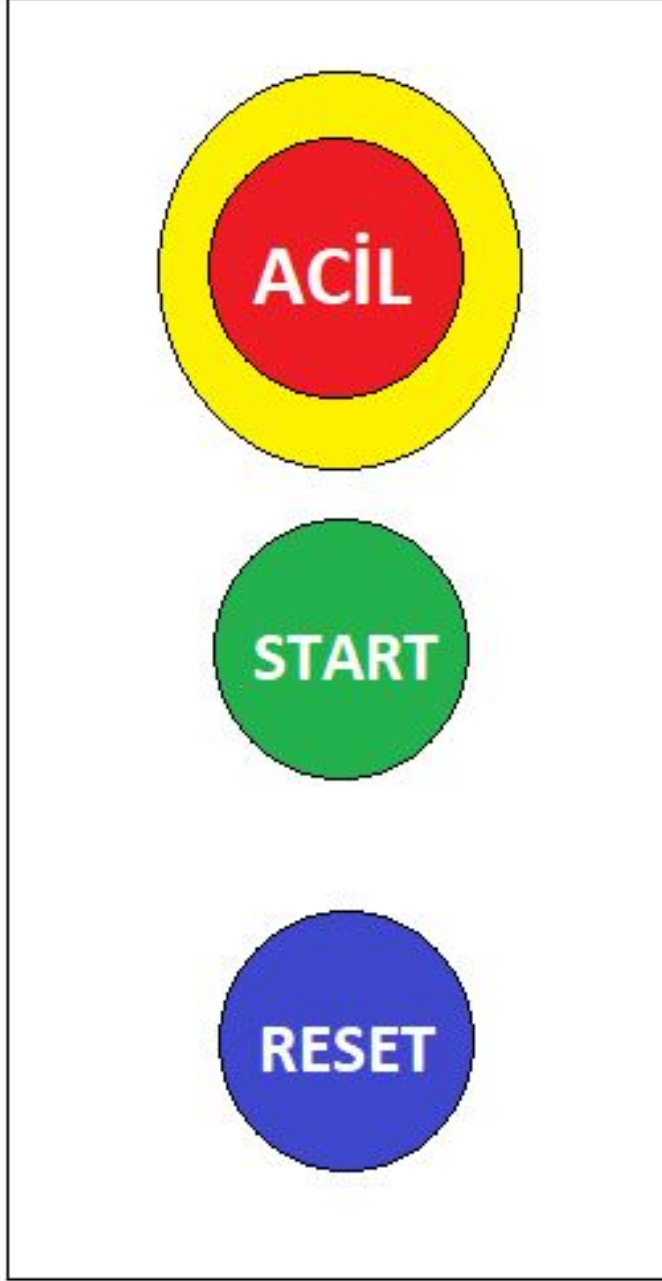

SİPARİŞ TARİHİ	
GÜNCELLEME TARİHİ	8.01.2023
PROJE SORUMLUSU	
MONTAJ SORUMLUSU	



 SRDR ROBOTİK TEL: +90 552 442 77 37 ADRES: Bağlarbaşı Mah. Yonca Sk. No:1 Kat:3/6 34844 Maltepe/İSTANBUL e-mail : info@srdrobotik.com

PROJE NO:	
KONTOL EDEN:	

KONTROL EDEN İMZA:

EK AÇIKLAMA:

25 BUTON_KUTUSU	
TOPLAM SAYFA SAYISI:	27
ÖNCEKİ SAYFA:	24 KAPİ_SWITCH
SONRAKİ SAYFA:	26 BUTON_KUTUSU-2

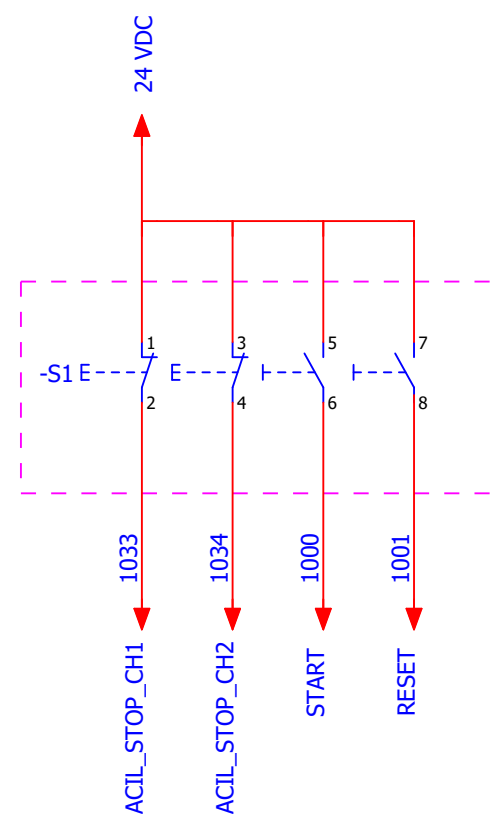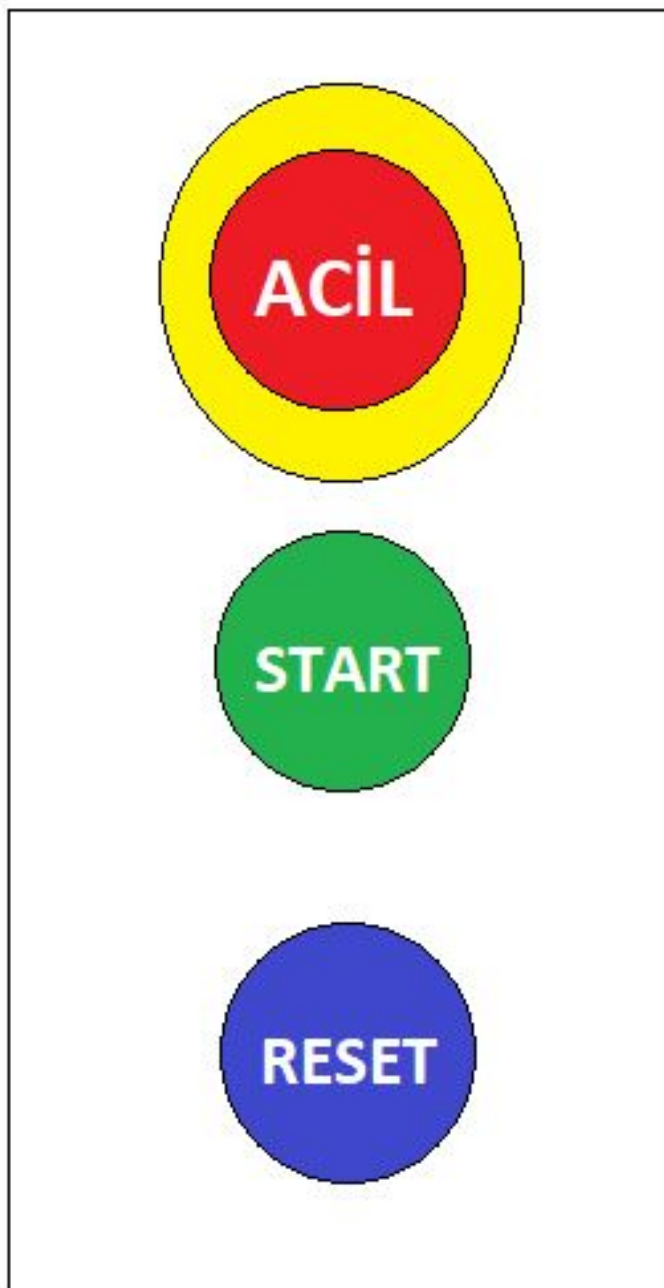

SİPARİŞ TARİHİ	
GÜNCELLEME TARİHİ	8.01.2023
PROJE SORUMLUSU	
MONTAJ SORUMLUSU	



SRDR ROBOTİK
 TEL: +90 552 442 77 37
 ADRES: Bağlarbaşı Mah. Yonca Sk. No:1 Kat:3/6 34844 Maltepe/İSTANBUL
 e-mail : info@srdrobotik.com

PROJE NO:

KONTOL EDEN:



KONTROL EDEN İMZA:

EK AÇIKLAMA:

26 BUTON KUTUSU-2

TOPLAM SAYFA SAYISI:	27
ÖNCEKİ SAYFA:	25 BUTON_KUTUSU
SÖNRAKİ SAYFA:	27 BUTON KUTUSU-3

Telif hakları ile korunmaktadır. Bu dokümanın başkalarına verilmesi ve çoğaltılması, içeriğinin değerlendirilmesi ve başkalarına bildirilmesi, aıkça izin verilmediđi sürece yasaktır.

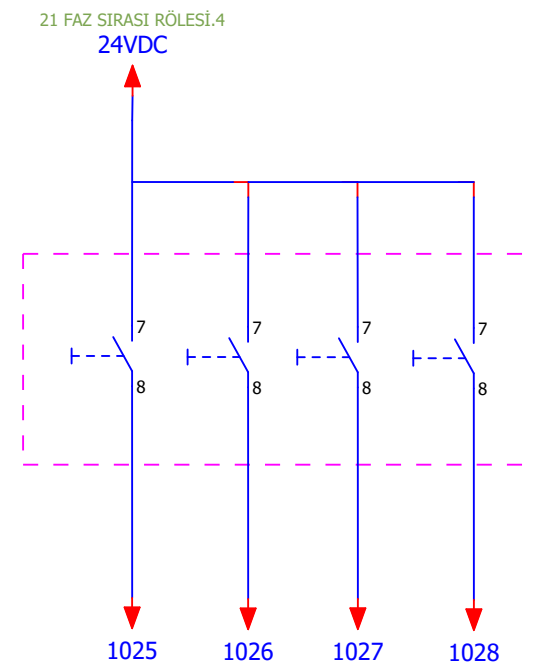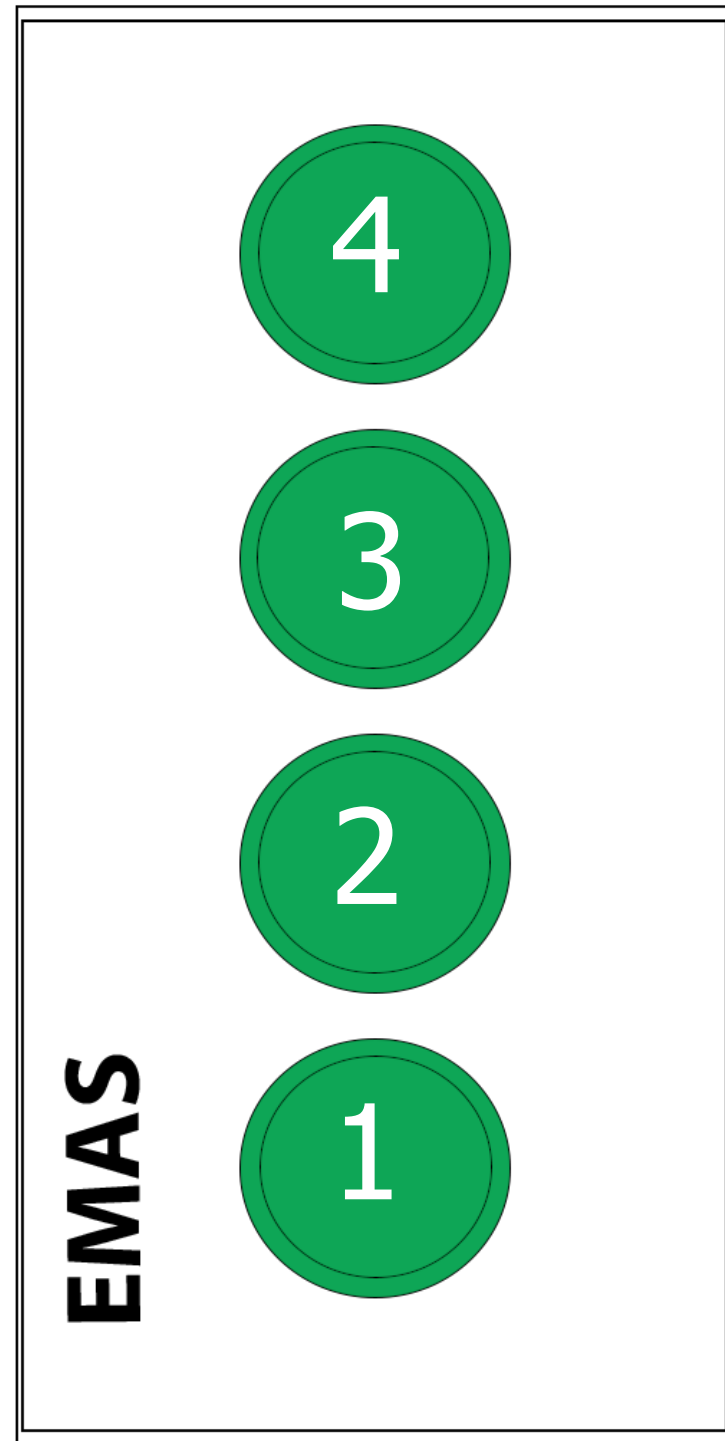

26 BUTON KUTUSU-2										28 KLEMENS GRUBU	
			Proje adı			BİRA			Proje numarası			IEC_bas003			EPLAN GmbH & Co. KG	

0	1	2	3	4	5	6	7	8	9		
X1: MAIN SUPPLY X2: 24 VDC X3: 0 VDC X4: RESERVE X5: ROBOT POWER X6: PLC INPUT X7: PLC OUTPUT X8: IŞIK BARİYERİ X9: KAPI SWITCH X10: IŞIK KOLONU X11: CNC -1 HABERLEŞME X12: CNC -2 HABERLEŞME X13: BUTON KUTUSU 1 X14: BUTON KUTUSU 2 X15: ROBOT HARD STOP - SOFT STOP X16: ROBOT SİNYALLERİ X17:BUTON KUTUSU 3 X18:FİKSTÜR SİNYALLERİ											
SİPARİŞ TARİHİ				 SRDR ROBOTİK TEL: +90 552 442 77 37 ADRES: Bağlarbaşı Mah. Yonca Sk. No:1 Kat:3/6 34844 Maltepe/İSTANBUL e-mail : info@srdrobotik.com		PROJE NO:		KONTROL EDEN İMZA:	EK AÇIKLAMA:	28 KLEMENS GRUBU	
GÜNCELLEME TARİHİ	12.01.2023										
PROJE SORUMLUSU						KONTOL EDEN:					
MONTAJ SORUMLUSU											
TOPLAM SAYFA SAYISI: 27 ÖNCEKİ SAYFA: 27 BUTON KUTUSU-3 SONRAKİ SAYFA:											